

Portfolio

Sein Pyae Htay

2026

Hello,

I’m Sein Pyae Htay

Drafter cum BIM Modeler

Advanced Diploma in Civil Engineering

City and Gulids London Institute (UK)

+959 400523608 (Whatsapp)

pyaepyae205200@gmail.com

https://www.linkedin.com/in/sein-pyae-htay



About Me

I am a Civil Engineering professional with approximately 3 years of experience in construction drafting, architectural documentation, and BIM modelling. I hold a Level 4 Diploma and Level 5 Advanced Diploma in Civil Engineering, with practical experience in both site engineering and technical drawing preparation.

I began my career as a Site Engineer cum Drafter and later progressed to BIM Modeler cum Drafter at King Construction. Throughout my professional experience, I have been involved in construction drawing preparation, site coordination, architectural drafting, 3D building modelling, and technical documentation.

My core technical expertise includes AutoCAD 2D Drafting and Autodesk Revit BIM Modelling, particularly in architectural and structural drawing development.

Through my experience, I have developed a good understanding of construction processes, drawing coordination, technical requirements, and project documentation. I am detail-oriented and responsible, with a strong commitment to producing accurate, high-quality technical drawings while continuously enhancing BIM capabilities and contributing to efficient construction and architectural projects.

MY CERTIFICATES

AutoCAD Intermediate



CERTIFICATE OF COMPLETION

CONGRATULATIONS!

You have successfully completed an Autodesk® Authorized Training Center® course specifically designed to satisfy your training requirements. Authorized Training Center instructors deliver quality–learning experiences with courses related to Autodesk products utilizing relevant content and comprehensive courseware. Autodesk's vision is to help people imagine, design, and create a better world.

Certificate No. AP702813098697555761782

MS SEIN PYAE HTAY		
NAME		
AUTOCAD (INTERMEDIATE)		AUTOCAD 2025
COURSE TITLE		PRODUCT
HSU MYAT HMWE	07-MARCH-2026	41-100 HOURS
INSTRUCTOR	COURSE DATE	COURSE DURATION

ZEON LIGHT TRAINING CENTRE
AUTODESK AUTHORIZED TRAINING CENTER

AUTODESK
Authorized Training Center

Autodesk, the Autodesk logo, and ATC are registered trademarks or trademarks of Autodesk, Inc., and/or its subsidiaries and/or affiliates in the USA and/or other countries. All other brand names, product names, or trademarks belong to their respective holders. Autodesk reserves the right to alter product and services offerings, and specifications and pricing at any time without notice, and is not responsible for typographical or graphical errors that may appear in this document. Autodesk did not provide this training course or any of the training materials. The Autodesk Learning Partner provided all course materials and training. © 2026 Autodesk, Inc. All rights reserved.

Professional Civil Engineering Completion Certificate



MY CERTIFICATES

Revit Architecture & Structure Essentail



CERTIFICATE OF COMPLETION

CONGRATULATIONS!

You have successfully completed an Autodesk® Authorized Training Center® course specifically designed to satisfy your training requirements. Authorized Training Center instructors deliver quality-learning experiences with courses related to Autodesk products utilizing relevant content and comprehensive courseware. Autodesk's vision is to help people imagine, design, and create a better world.

Certificate No. AP702813098658015761782

MS SEIN PYAE HTAY		
NAME		
REVIT ARCHITECTURE & STRUCTURE ESSENTIAL		REVIT 2025
COURSE TITLE		PRODUCT
PYAE PHYO ZAW	09-FEBRUARY-2026	41-100 HOURS
INSTRUCTOR	COURSE DATE	COURSE DURATION

ZEON LIGHT TRAINING CENTRE
AUTODESK AUTHORIZED TRAINING CENTER

AUTODESK
Authorized Training Center


Autodesk, the Autodesk logo, and ATC are registered trademarks or trademarks of Autodesk, Inc., and/or its subsidiaries and/or affiliates in the USA and/or other countries. All other brand names, product names, or trademarks belong to their respective holders. Autodesk reserves the right to alter product and services offerings, and specifications and pricing at any time without notice, and is not responsible for typographical or graphical errors that may appear in this document. Autodesk did not provide this training course or any of the training materials. The Autodesk Learning Partner provided all course materials and training. © 2026 Autodesk, Inc. All rights reserved.

Professional Civil Engineering Achievement Certificate (2nd Award)



MY CERTIFICATES

SketchUp Certificate

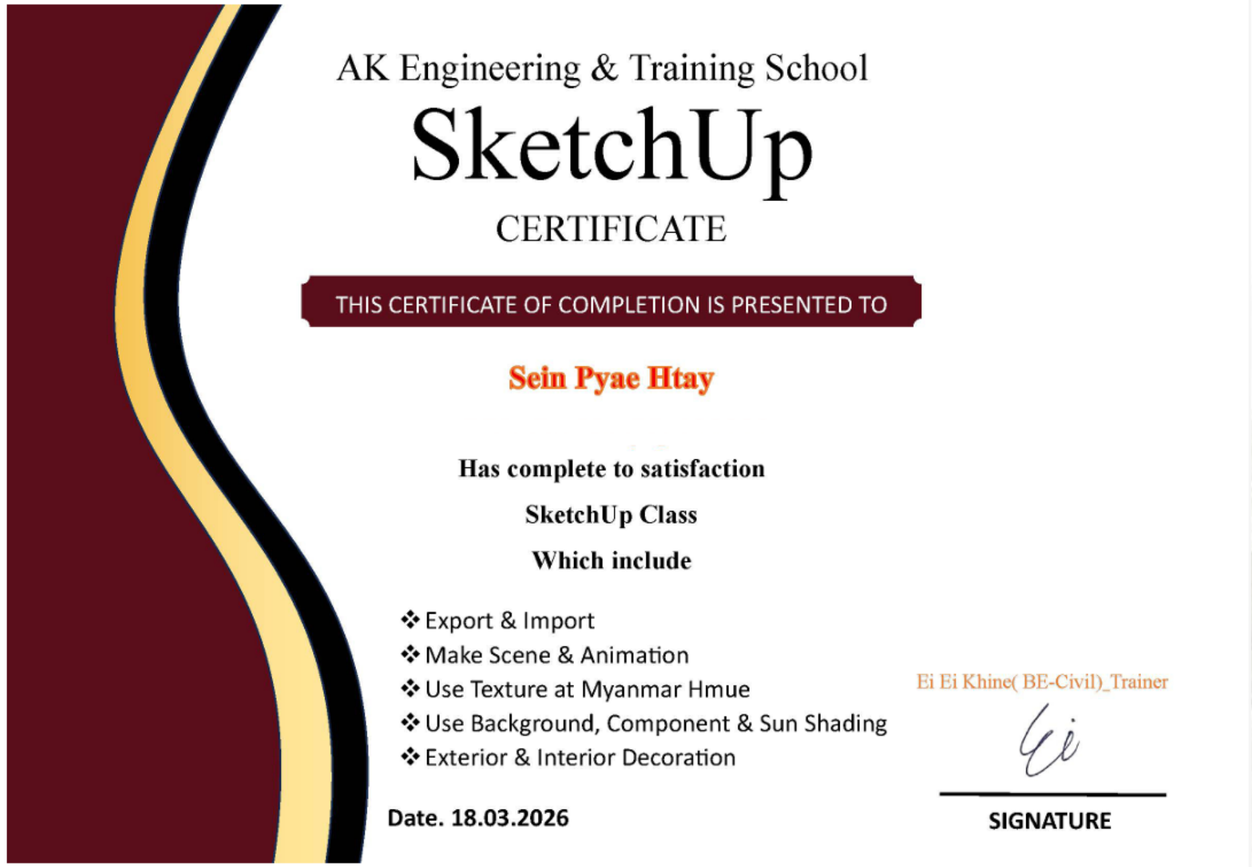

AK Engineering & Training School

SketchUp

CERTIFICATE

THIS CERTIFICATE OF COMPLETION IS PRESENTED TO

Sein Pyae Htay

Has complete to satisfaction

SketchUp Class

Which include

- Export & Import
- Make Scene & Animation
- Use Texture at Myanmar Hmue
- Use Background, Component & Sun Shading
- Exterior & Interior Decoration

Date. 18.03.2026

Ei Ei Khine(BE-Civil)_Trainer

SIGNATURE

Professional Graphic Design Certificate



GCTI

Certificate of Training

This certificate is proudly presented to

Sein Pyae Htay

for successfully completing the

Professional Graphic Design Course

at GENESYS COMPUTER & TECHNOLOGY INSTITUTE

Given on the 15th day of December 2023

A

GRADE

GENESYS COMPUTER & TECHNOLOGY INSTITUTE Reg No:126076886

Head of Instructors and President of GCTI

Education

City & Gulids London Institute 2023 - 2026

- Level 5 - Advanced Diploma in Civil Engineering (Distinction) (2025 - 2026)
- Level 4 - Diploma in Civil Engineering (2024 - 2025)
- Level 3 - Diploma in Civil Engineering & Foundation (2023 - 2024)

University Of the People 2024 - 2026

- Associate Degree in Business Administration (High honrs)

Language

- English (Intermediate)
- Chinese (Basic & Continue Learning)
- Burmese (Native)

Software Proficiency

- AutoCAD 
- Revit 
- Sketchup 
- Tekla 
- Adobe Photoshop 
- Microsoft Project 
- Microsoft Office (Word, Excel, Powerpoint)
- Canva 

Software Proficiency

AutoCAD – Intermediate

- 2D architectural drafting
- Floor plans, elevations and sections
- Layers, dimensions and annotations
- Blocks and drawing organization
- Layout setup and plotting
- Drawing revisions

Autodesk Revit – Basic to Intermediate

- 3D architectural modelling
- Walls, floors, roofs and ceilings
- Doors and windows
- Stairs and building components
- Floor plans, elevations and sections
- Sheet creation and documentation
- Basic family modification and creation

Other Softwares

- SketchUp – 3D modelling
- Tekla - Basic knowledge of structural modelling
- Adobe Photoshop – Basic image editing
- Microsoft Project - Project scheduling, task tracking and Gantt charts
- Microsoft Excel – Documentation and spreadsheets
- Microsoft Word – Technical documentation
- Microsoft PowerPoint – Presentations
- Canva – Presentation design

Selected Projects

- This portfolio showcases a selection of my personal, professional, and freelance projects, highlighting my skills in architectural drafting, BIM modelling, and 3D visualization.
- The main focus is on architectural drawings developed using Autodesk AutoCAD 2024, BIM projects created with Autodesk Revit 2024, and 3D modelling and visualization projects using SketchUp 2024, covering residential, commercial, hotel, interior, and exterior designs.

Portfolio Overview

1. Three Storey RCC Residential Building
   Autodesk AutoCAD 2024
2. Three and Half Storey Residential Building
   Autodesk AutoCAD 2024
3. One Storey RCC Building
   Autodesk AutoCAD 2024
4. Three and Half Storey Residential Building ISO Drawing
   Autodesk AutoCAD 2024
5. Three Storey with Penthouse Building Project
   Autodesk AutoCAD 2024
6. Three Storey RCC Residential Building
   Autodesk AutoCAD 2024
7. Five Storey Hotel Project
   Autodesk AutoCAD 2024

Portfolio Overview

8. Three and Half Stories Residential Building
   Autodesk Revit 2024
9. Mix Used Building Project
   Autodesk Revit 2024
10. Toilet Setting Out Model
    Autodesk Revit 2024
11. Two Storey Building Project
    Sketchup 2024
12. Guest House – Exterior 3D Modelling
    Sketchup 2024
13. Monastery Project
    Sketchup 2024
14. Other Projects
    Sketchup 2024 & Tekla Structural Designer

Project 01

- Residential Design: Three Storey RCC Building
- Location:Yangon, Myanmar
- Software: AutoCAD & SketchUp 2024
- Type: Residential




- Project - Residential Building 3D Model
- Scope - Exterior 3D Modeling
- Software - Sketchup 2024










- Drawings - Layout Plan, Detail Drawing & Elevation
- Software - Autodesk AutoCAD 2024

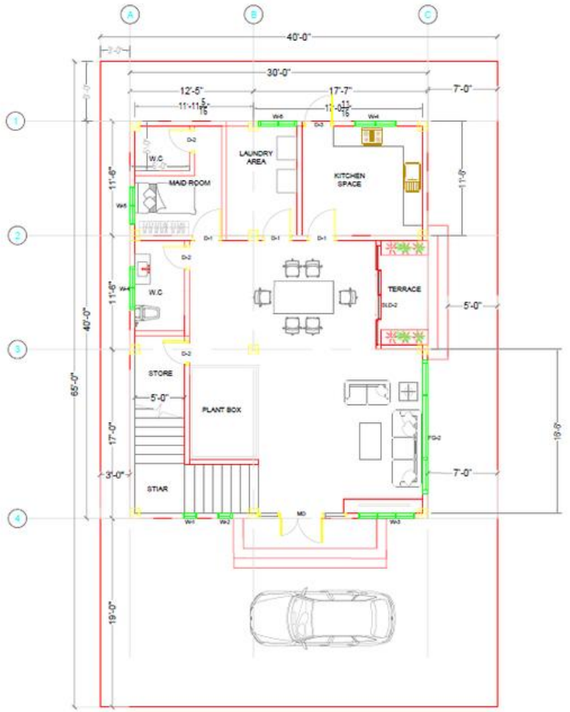


BUILDING LAYOUT PLAN

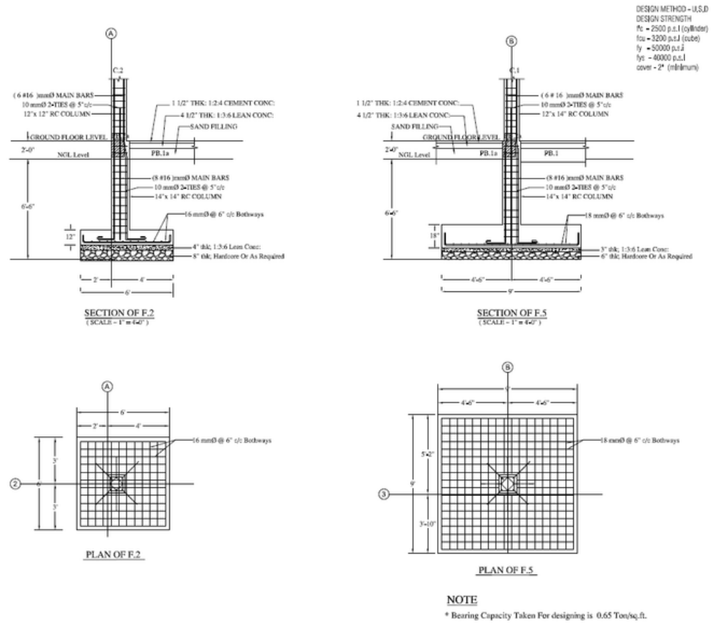


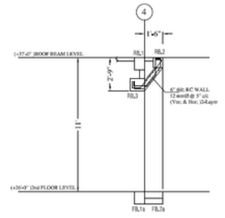


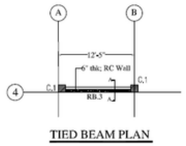

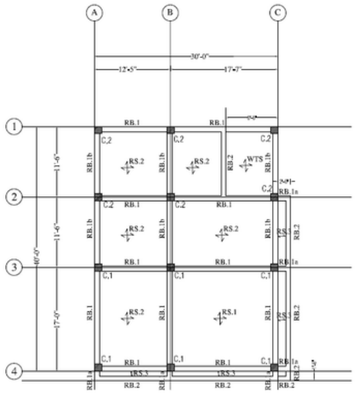



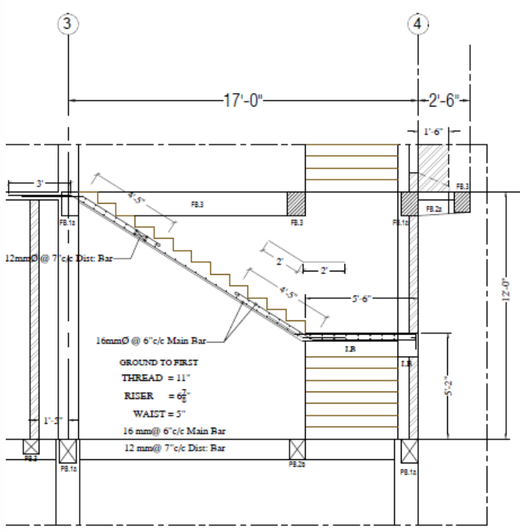

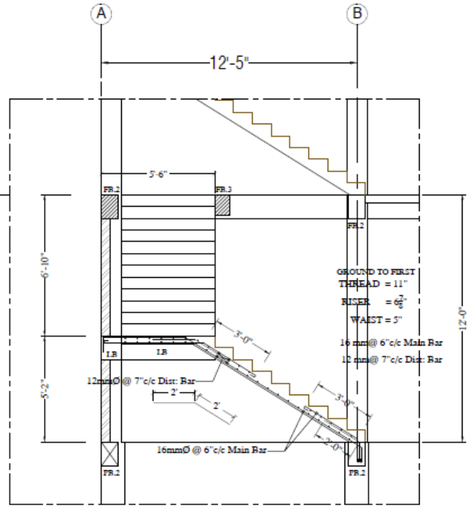

STAIR DETAIL




Project 2


- Residential Design: Three and Half Storey Residential Building
- Location:Yangon, Myanmar
- Software: AutoCAD & SketchUp 2024
- Type: Residential







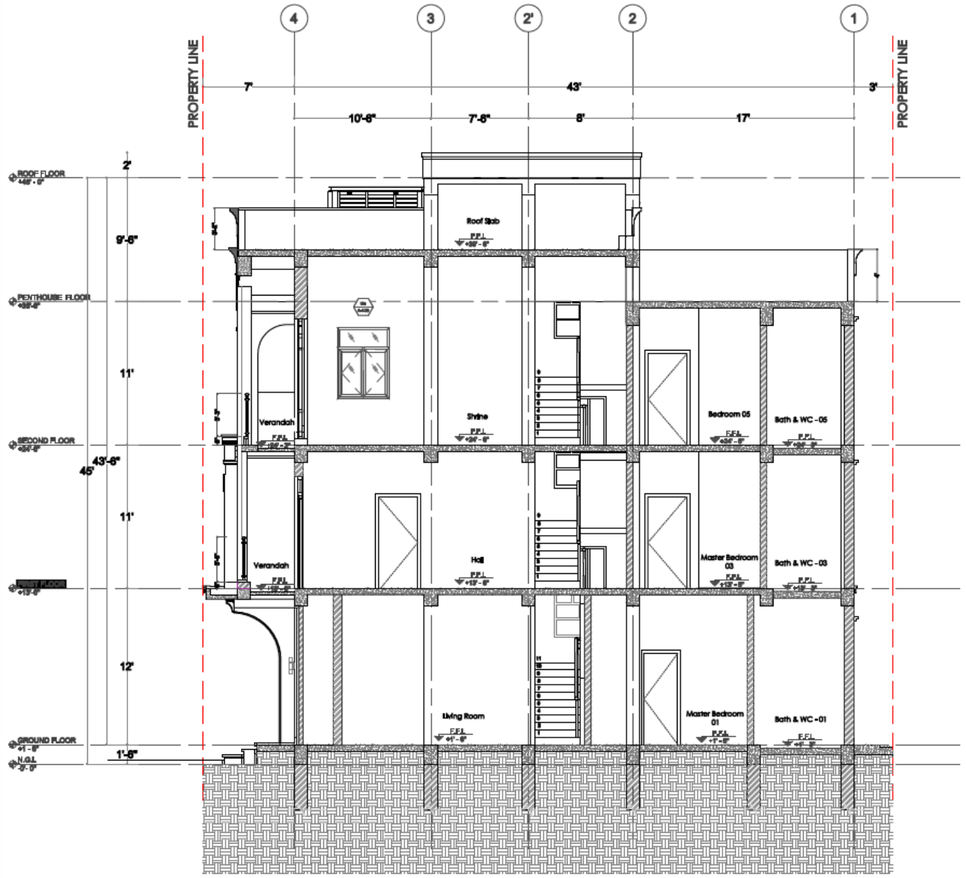

- Drawings - Plan, Detail Drawing, Section & Elevation
- Software - Autodesk AutoCAD 2024

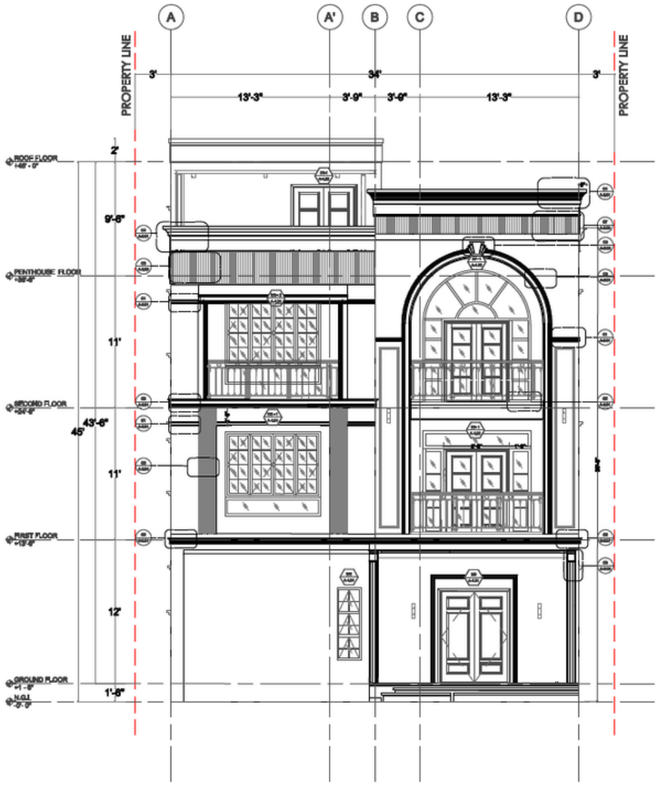

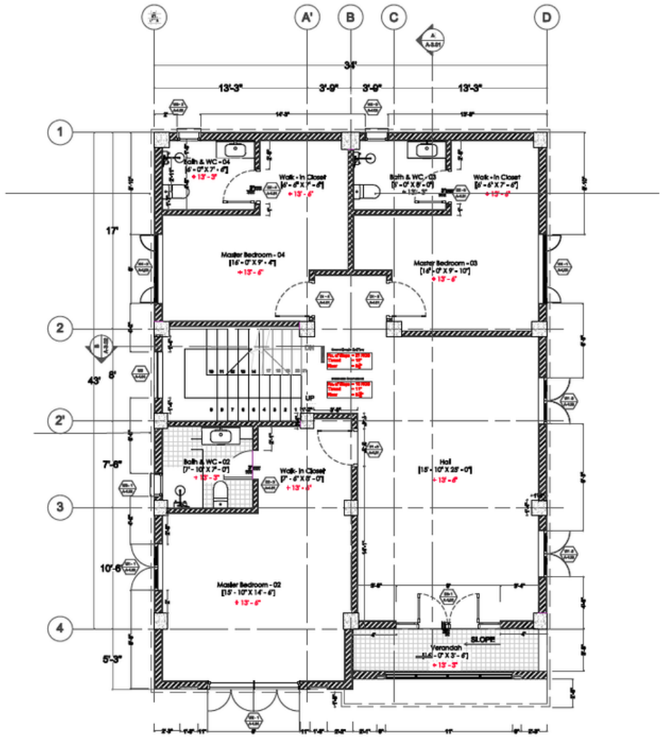

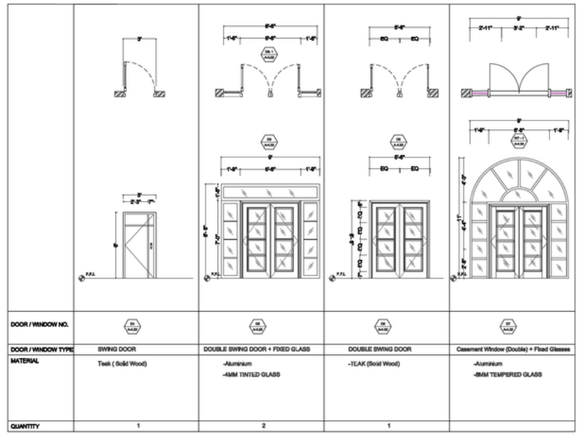


Project 3







- Residential Design: One Storey RCC Building
- Location: Toon Tay, Myanmar
- Software: AutoCAD & SketchUp 2024
- Type: Residential

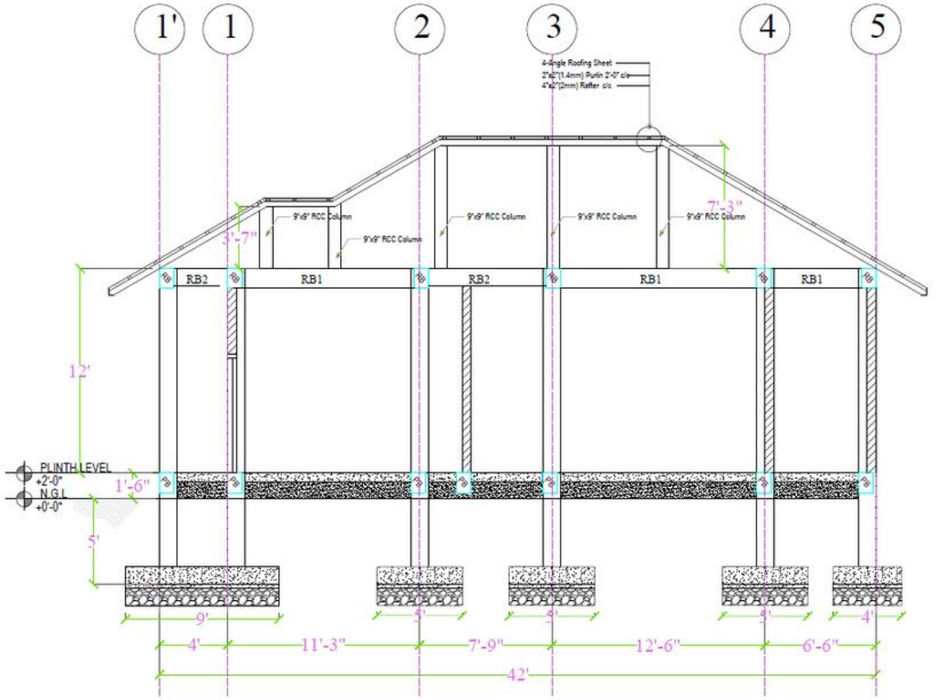


CROSS-SECTION

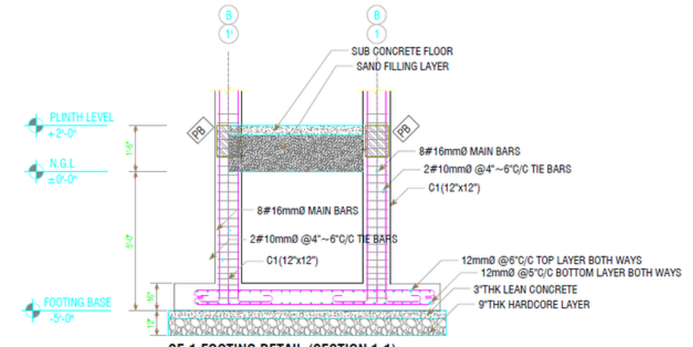

CF-1 FOOTING DETAIL (SECTION 1-1)

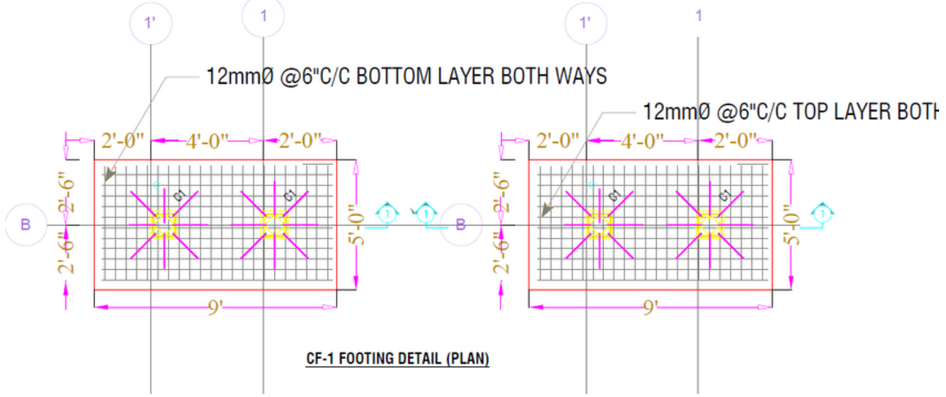

CF-1 FOOTING DETAIL (PLAN)

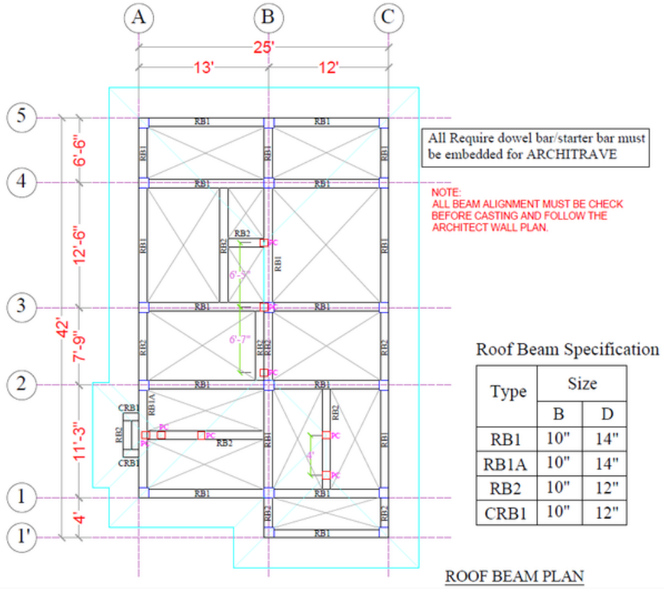

All Require dowel bar/starter bar must be embedded for ARCHITRAVE













NOTE:
ALL BEAM ALIGNMENT MUST BE CHECK BEFORE CASTING AND FOLLOW THE ARCHITECT WALL PLAN.

Roof Beam Specification

Type	Size	
	B	D
RB1	10"	14"
RB1A	10"	14"
RB2	10"	12"
CRB1	10"	12"

ROOF BEAM PLAN

PLINTH BEAM SECTIONS

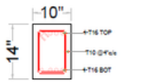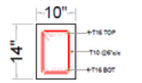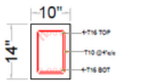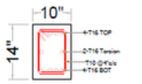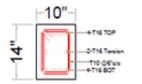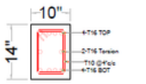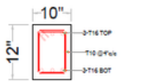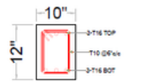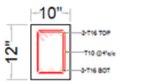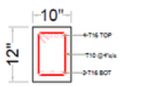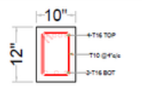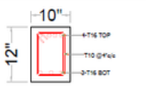LEFT	MID	RIGHT
		
PB-1	PB-1	PB-1
		
PB-1A	PB-1A	PB-1A
		
PB-2	PB-2	PB-2
		
CPB-1	CPB-1	CPB-1


Project 4

- Residential Design: Three and Half Storey Residential Building
- Location:Yangon, Myanmar
- Software: AutoCAD 2024
- Type: Residential








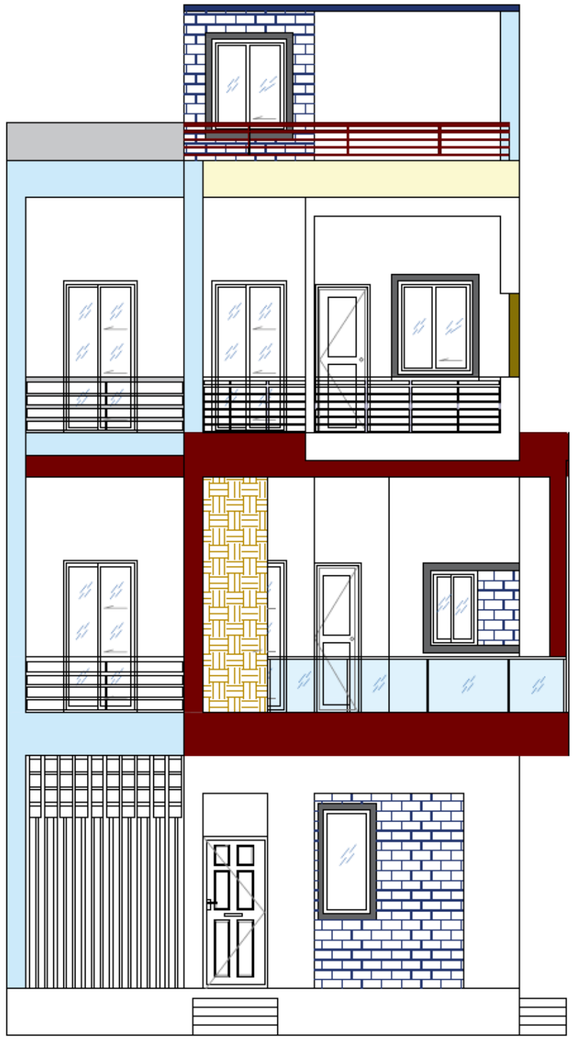


Front Elevation View

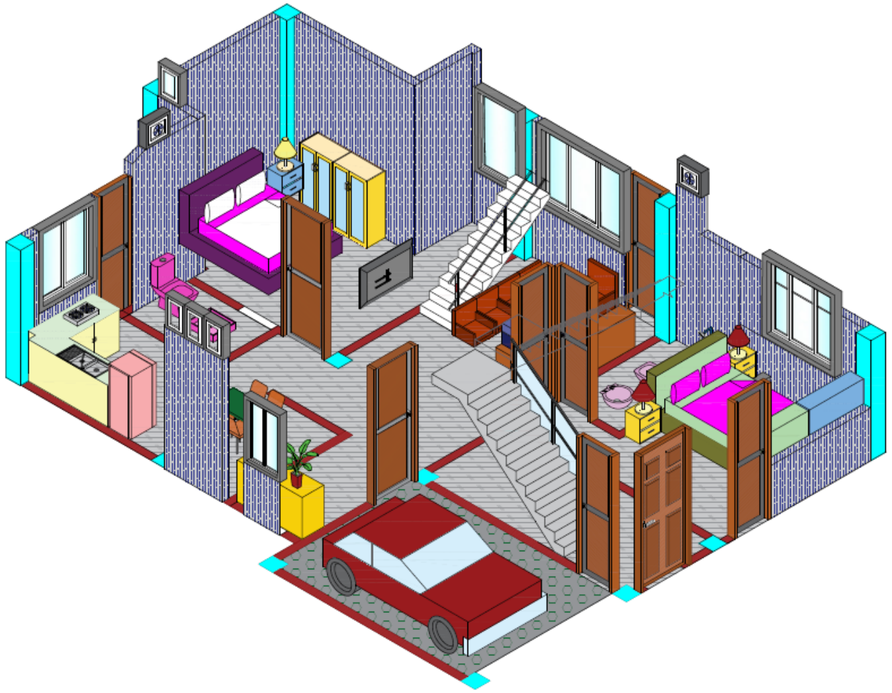



Door and Window Details

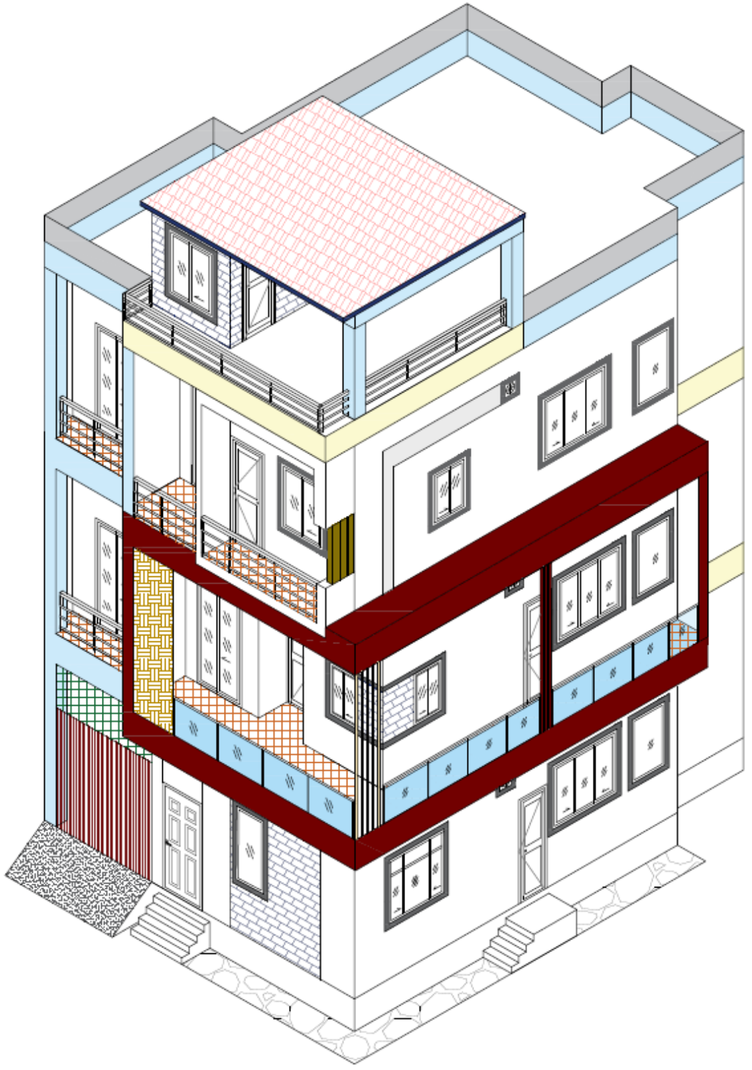



ISOMETRIC VIEW





Project 05


- Residential Design: Three Storey with Penthouse Building Project
- Location: Yangon, Myanmar
- Software: AutoCAD 2024
- Type: Residential

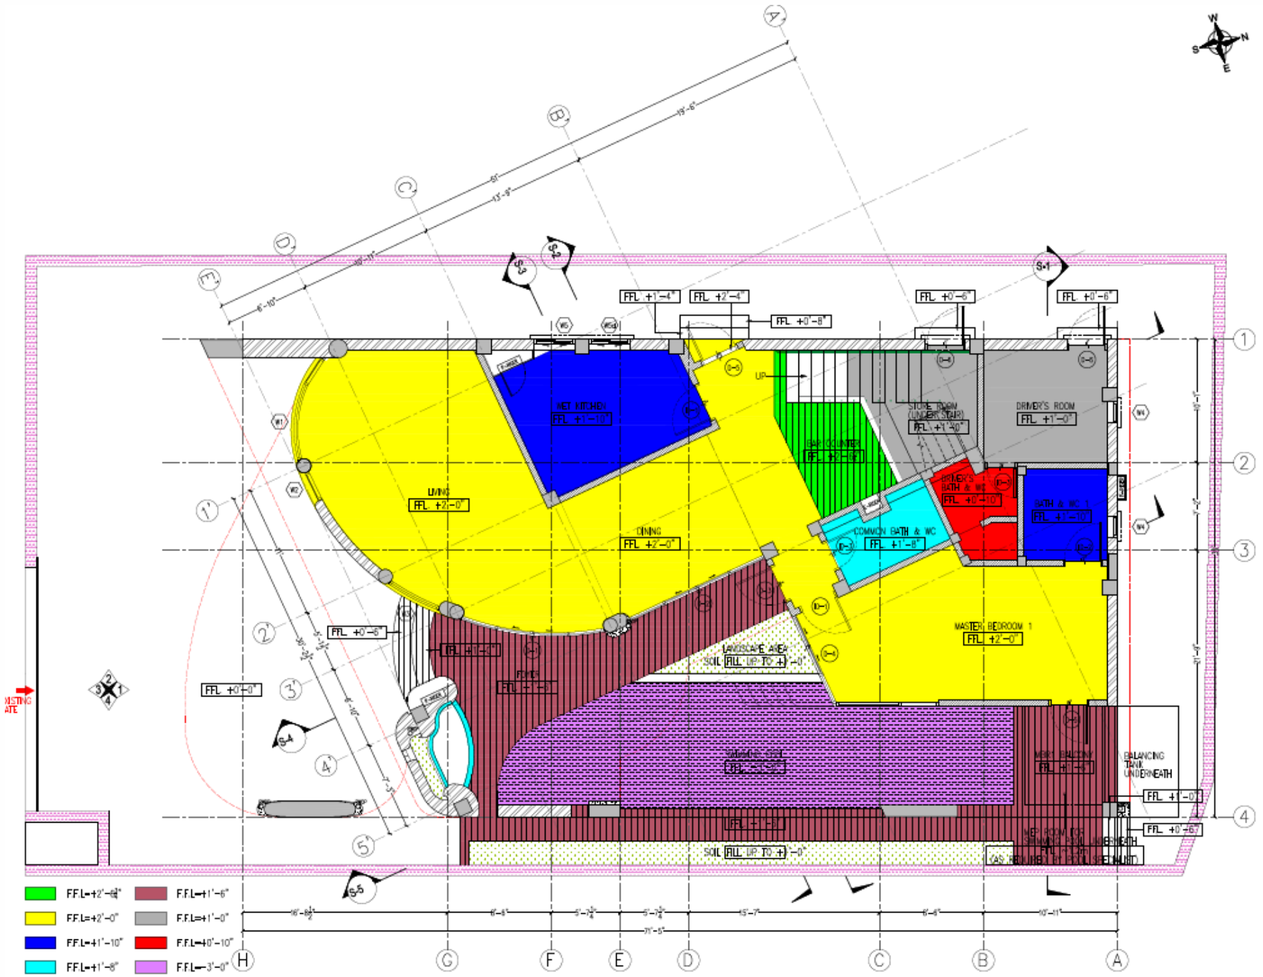

WET KITCHEN
FFL +1'-10"
LIVING
FFL +2'-0"
DINING
FFL +2'-0"
BAR COUNTER
FFL +2'-4"
TOILET ROOM (UNDER STAIR)
FFL +1'-10"
DRIVER'S ROOM
FFL +1'-0"
PROJECTED BATH & WC
FFL +0'-10"
COMMON BATH & WC
FFL +1'-8"
BATH & WC 1
FFL +1'-10"
MASTER BEDROOM 1
FFL +2'-0"
LANDSCAPE AREA
SOIL FILL UP TO +0'-0"
FFL +0'-6"
FFL +0'-0"
MOTOR HOUSE
FFL +1'-0"
SUMP
FFL -3'-0"
BALANCING TANK UNDERNEATH
SOIL FILL UP TO +0'-0"
MEETING GATE
F.F.L=+2'-4"
F.F.L=+2'-0"
F.F.L=+1'-10"
F.F.L=+1'-8"
F.F.L=+1'-6"
F.F.L=+1'-0"
F.F.L=+0'-10"
F.F.L=-3'-0"

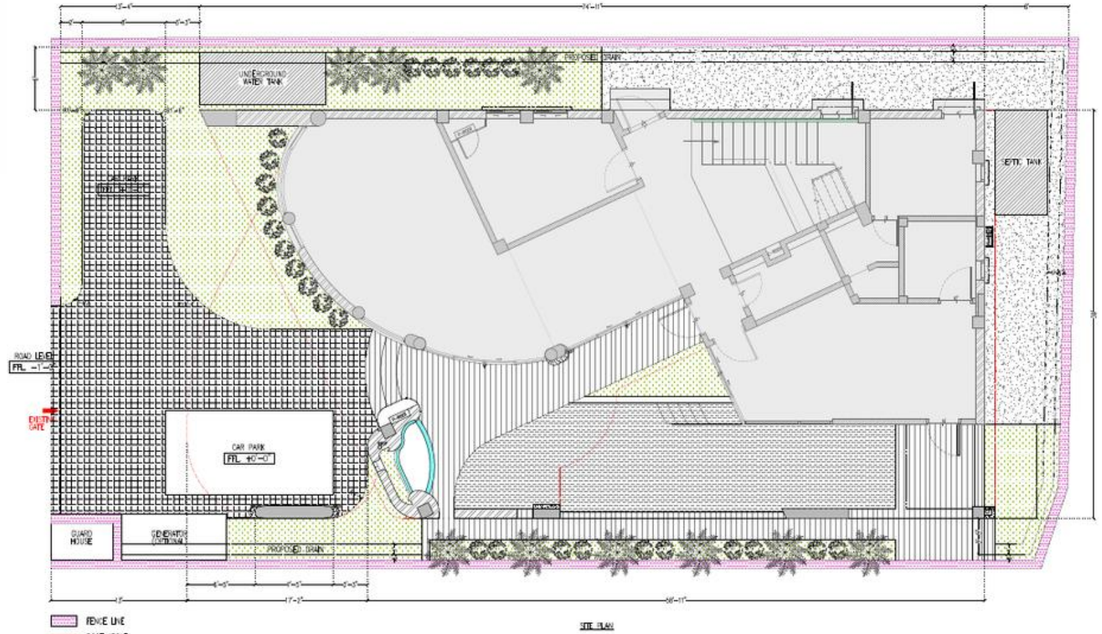

UNDERGROUND WATER TANK
SEPTIC TANK
ROAD LEVEL
FFL -1'-3"
EXISTING GATE
CAR PARK
FFL +0'-0"
GUARD HOUSE
GENERATOR (OPTIONAL)
PROPOSED DRAIN
FENCE LINE
ROOF ABOVE
GRASS
CONCRETE FLOORING
OUTDOOR TILE
SITE PLAN

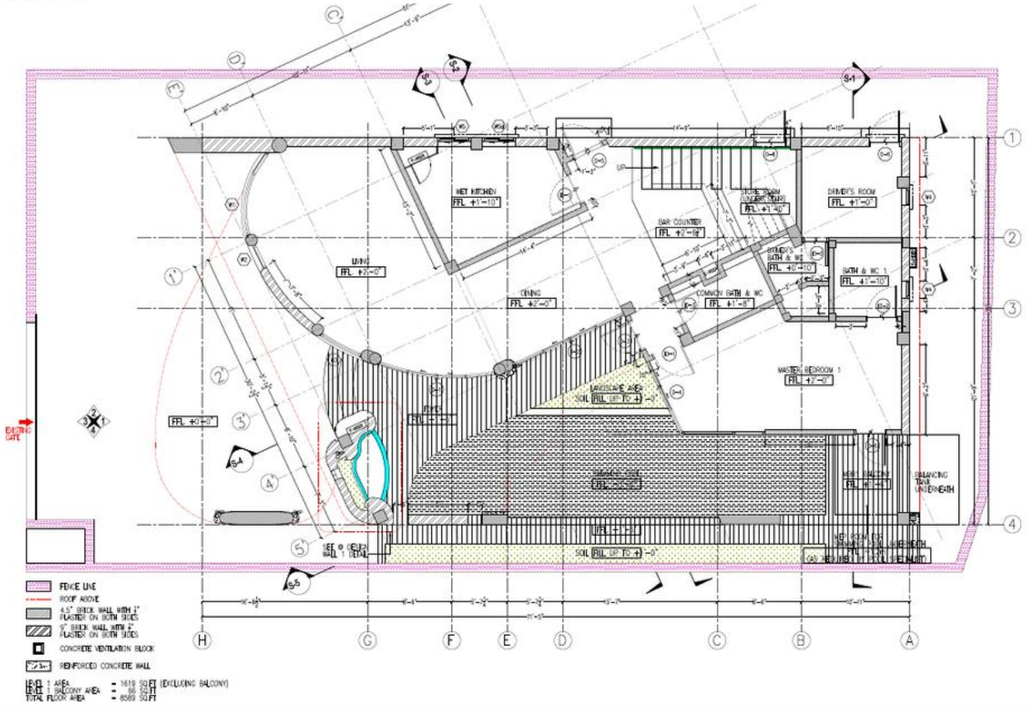
WET KITCHEN
FFL +1'-10"
LIVING
FFL +2'-0"
DINING
FFL +2'-0"
BAR COUNTER
FFL +2'-4"
TOILET ROOM (UNDER STAIR)
FFL +1'-10"
DRIVER'S ROOM
FFL +1'-0"
PROJECTED BATH & WC
FFL +0'-10"
COMMON BATH & WC
FFL +1'-8"
BATH & WC 1
FFL +1'-10"
MASTER BEDROOM 1
FFL +2'-0"
LANDSCAPE AREA
SOIL FILL UP TO +0'-0"
FFL +0'-0"
SUMP
FFL -3'-0"
MOTOR HOUSE
FFL +1'-0"
BALANCING TANK UNDERNEATH
SOIL FILL UP TO +0'-0"
EXISTING GATE
FENCE LINE
ROOF ABOVE
9" BRICK WALL WITH 1" PLASTER ON BOTH SIDES
5" BRICK WALL WITH 1" PLASTER ON BOTH SIDES
CONCRETE VENTILATION BLOCK
REINFORCED CONCRETE WALL
LEVEL 1 AREA = 1618 SQ.FT (EXCLUDING BALCONY)
LEVEL 1 BALCONY AREA = 66 SQ.FT
TOTAL FLOOR AREA = 8589 SQ.FT

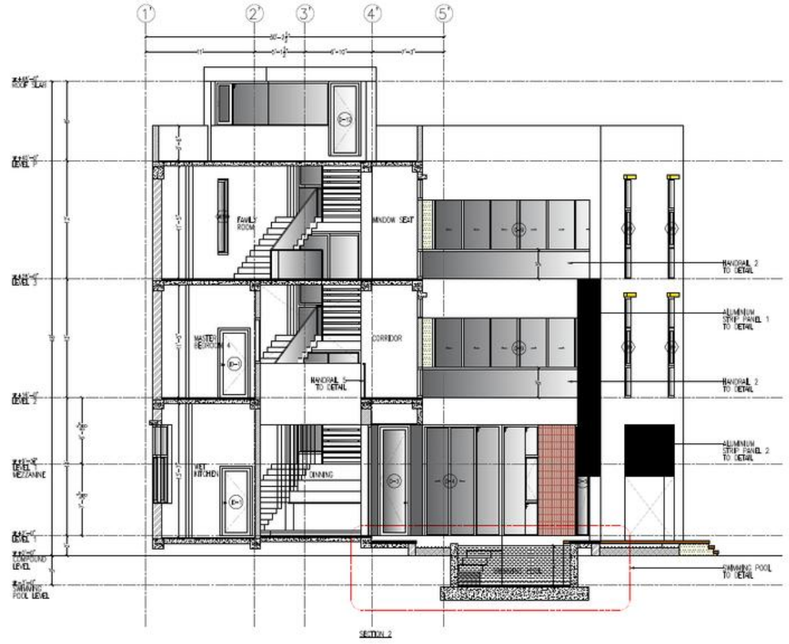
1
2
3
4
5
FAMILY ROOM
WINDOW SEAT
MASTER BEDROOM
CORRIDOR
WET KITCHEN
RAILING 2 TO DETAIL
ALUMINUM STRIP PANEL 1 TO DETAIL
RAILING 3 TO DETAIL
RAILING 2 TO DETAIL
ALUMINUM STRIP PANEL 2 TO DETAIL
SWIMMING POOL TO DETAIL
SECTION 2

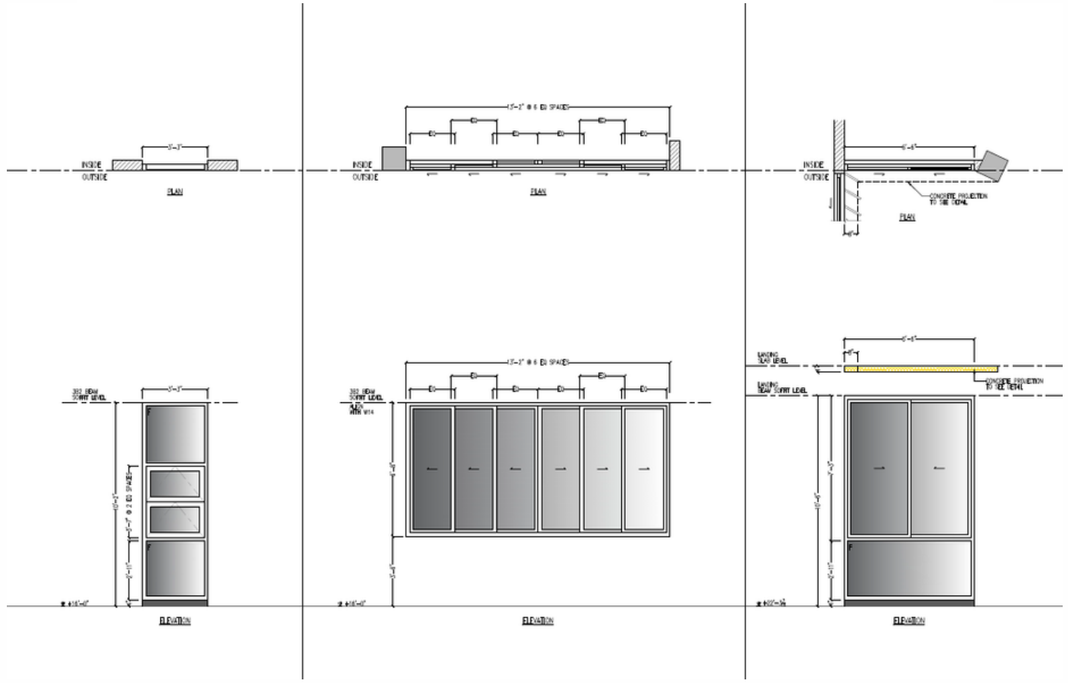
INSIDE
OUTSIDE
PLAN
PLAN
CONCRETE PROJECTION TO SEE DETAIL
PLAN
ELEVATION
ELEVATION
ELEVATION

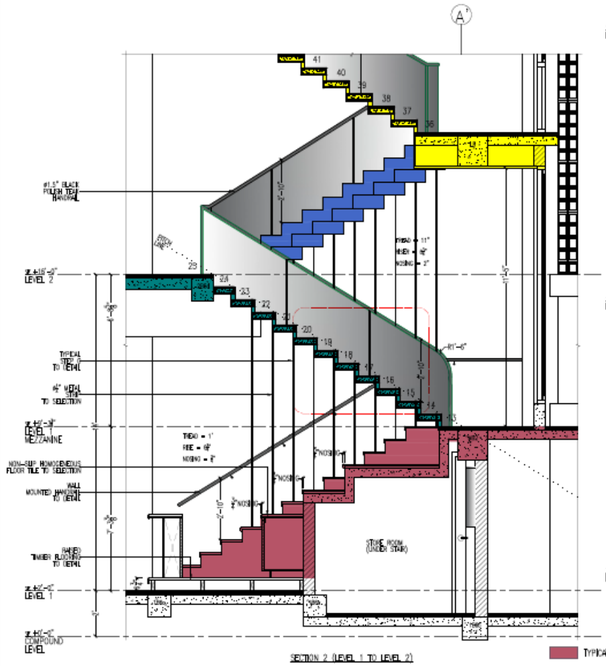
A
A'
#1.5" BLACK FULLER TEXT RAILING
TYPICAL TREAD TO DETAIL
4" RISER TYPE TO SELECTION
NON-SLIP REINFORCEMENT FLOOR TILE TO SELECTION
WALL MOUNTED HANDRAIL TO DETAIL
PAINTED TIMBER BLADDERS TO DETAIL
STONE WORK (UNDER STAIR)
TYPICAL STEP A
TYPICAL STEP B
TYPICAL STEP C
TYPICAL STEP D
SECTION 2 (LEVEL 1 TO LEVEL 2)

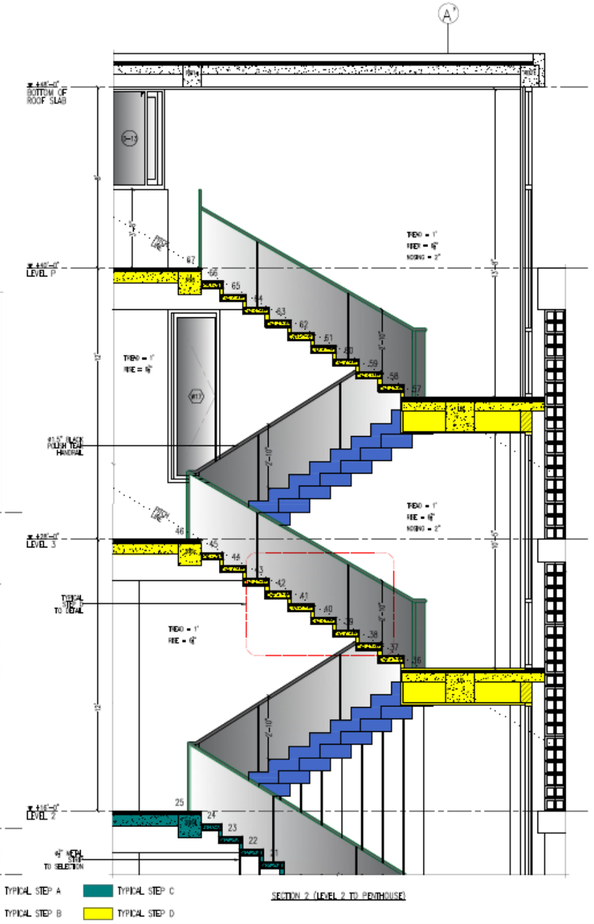
A
A'
#1.5" BLACK FULLER TEXT HANDRAIL
TYPICAL TREAD TO DETAIL
4" RISER TYPE TO SELECTION
SECTION 2 (LEVEL 2 TO PENTHOUSE)


Project 06









- Residential Design: Three Storey RCC Residential Building
- Location: Mandalay, Myanmar
- Software: AutoCAD 2024
- Type: Residential

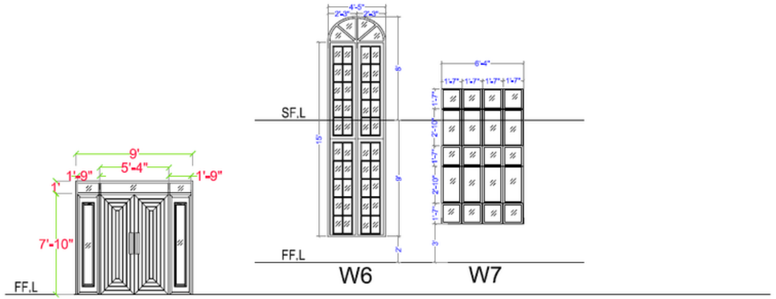


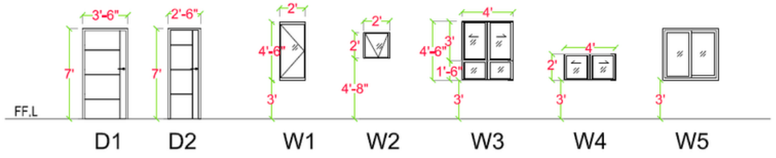


DOOR AND WINDOW DETAILS

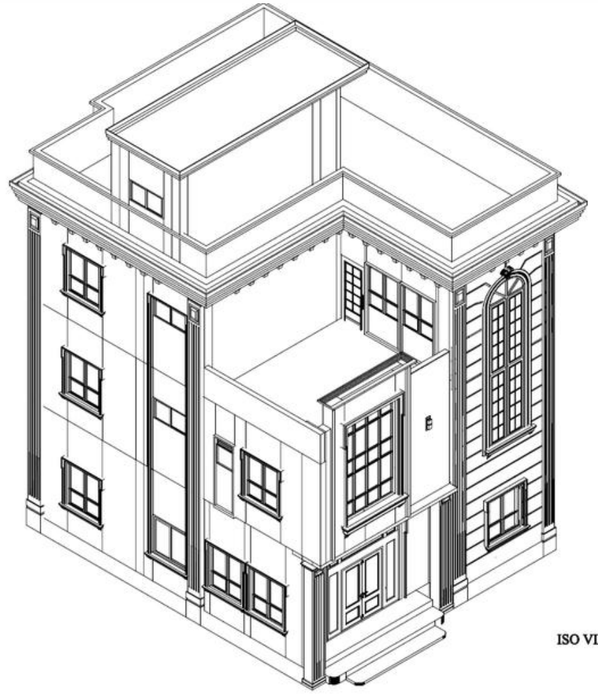


ISO VIEW

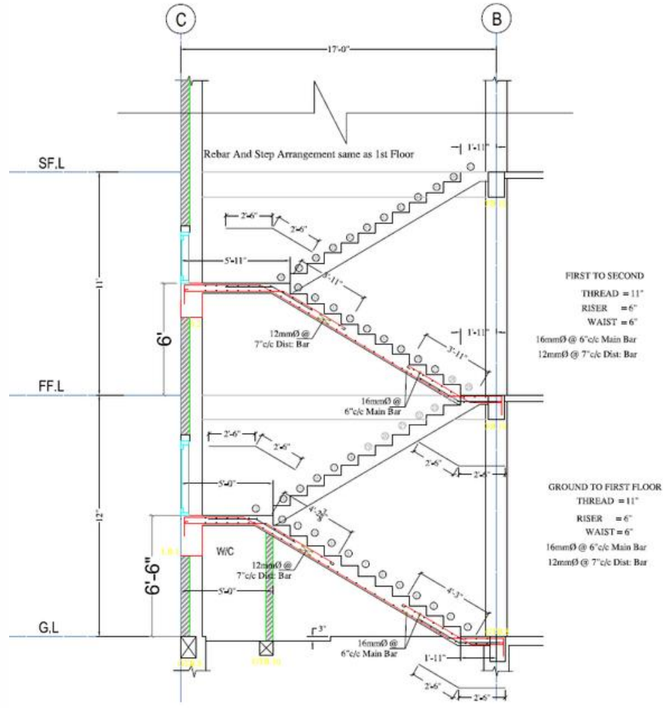

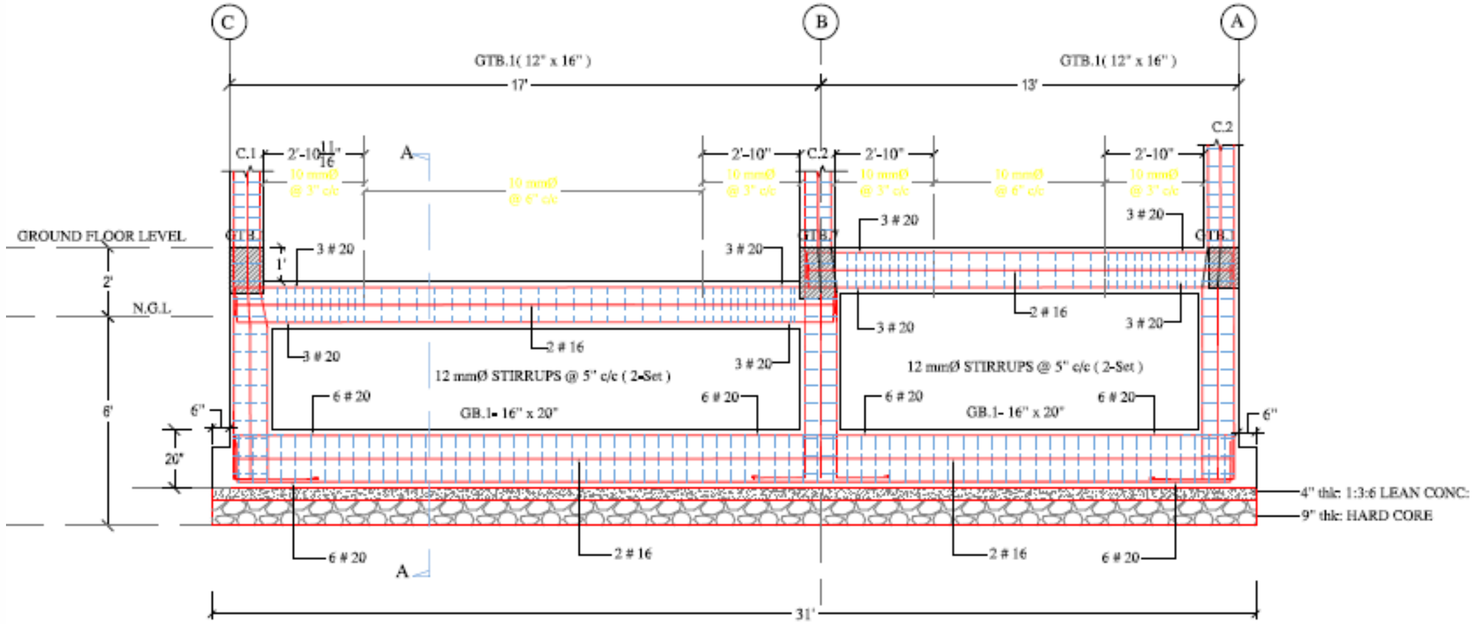

LONGITUDINAL SECTION OF GB.1 .

(SCALE ~ 1" = 4'-0")

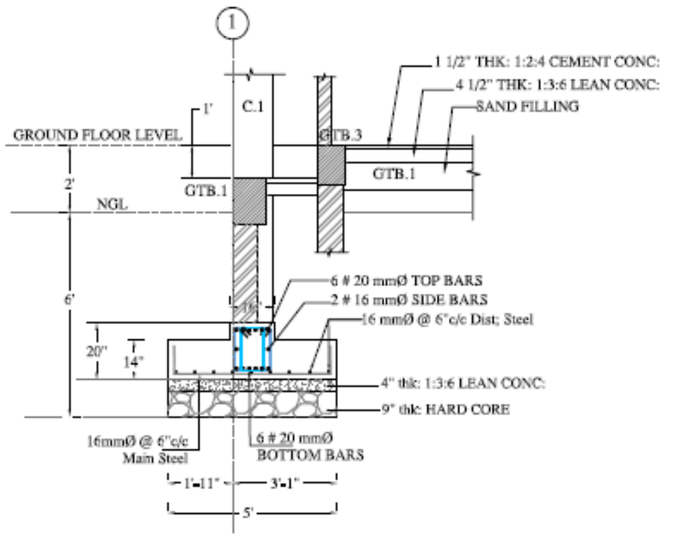



SECTION: A-A


(SCALE ~ 1" = 4'-0")

Project 07

- Residential Design: Five Storey Hotel Project
- Project Type: Personal Project
- Location: Myanmar
- Software: AutoCAD 2024
- Type: Residential

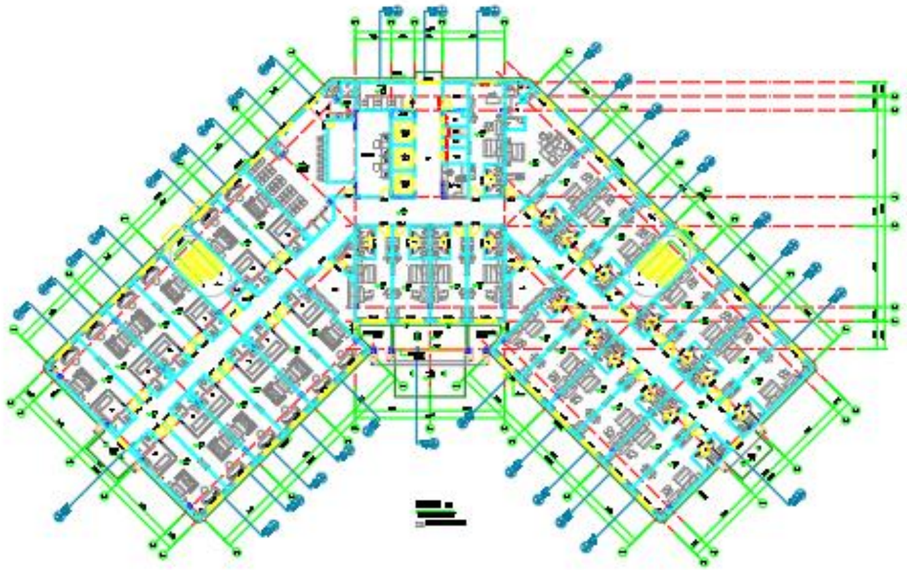


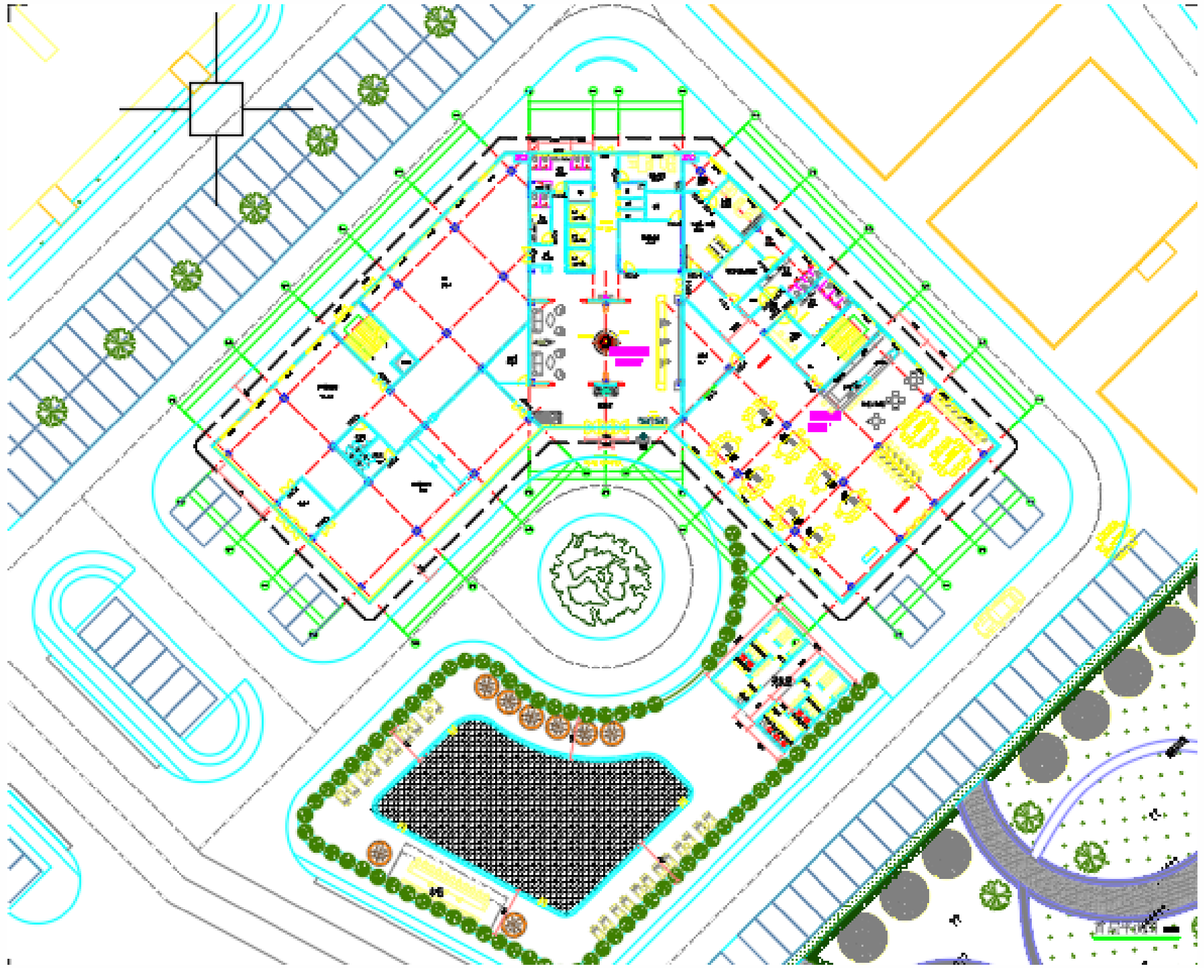


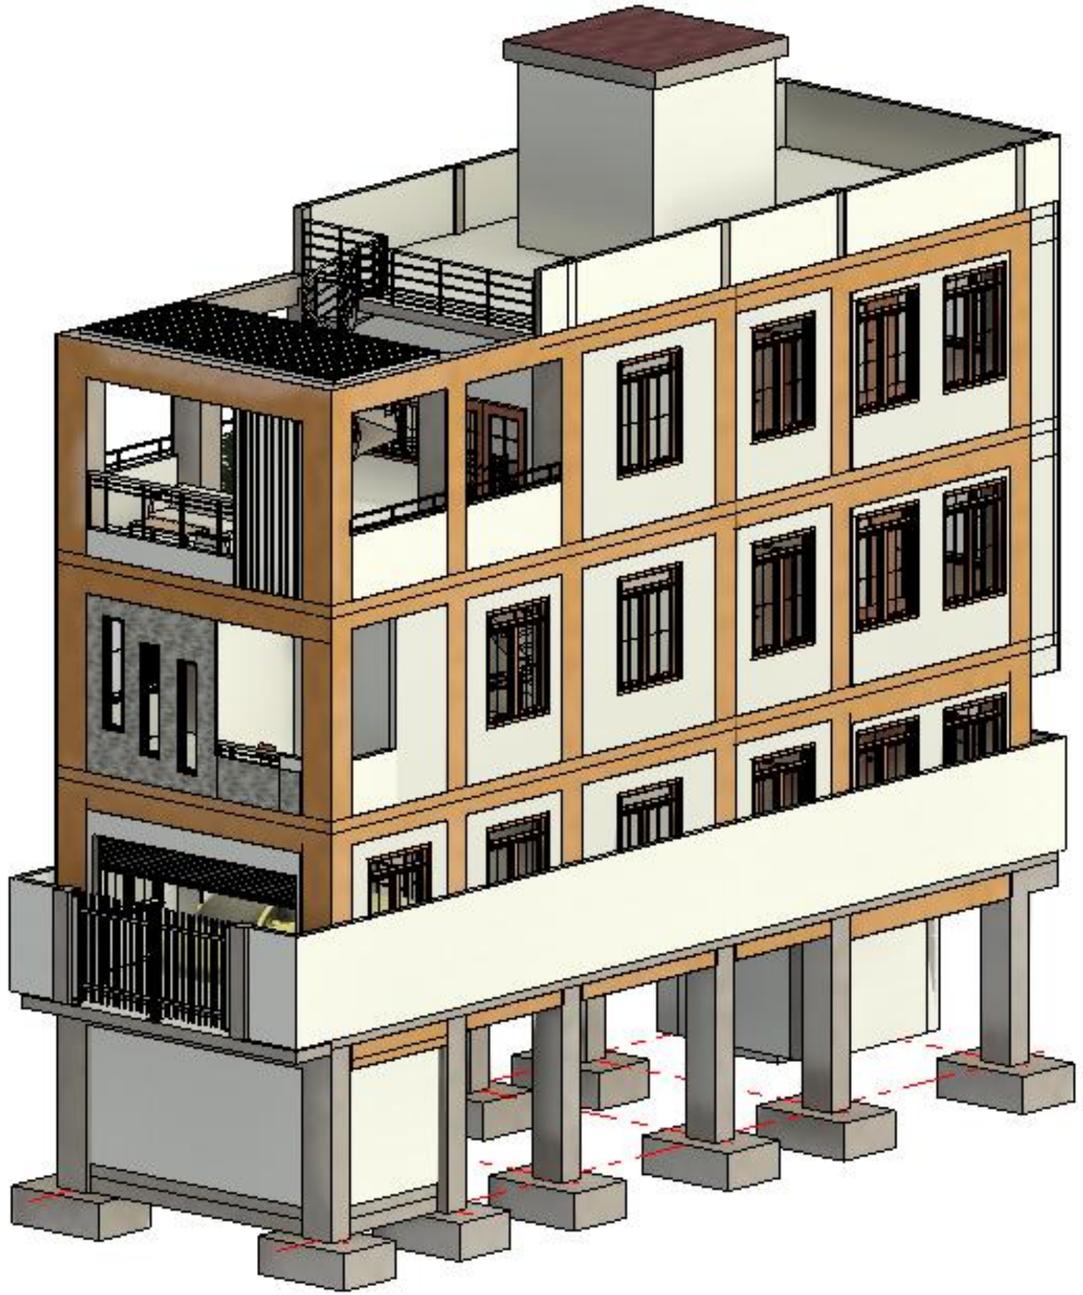



Project 08

- Residential Design: Three and Half Stories Residential Building
- Project Type: Personal Project
- Location: Myanmar
- Software: Autodesk Revit 2024
- Type: Residential

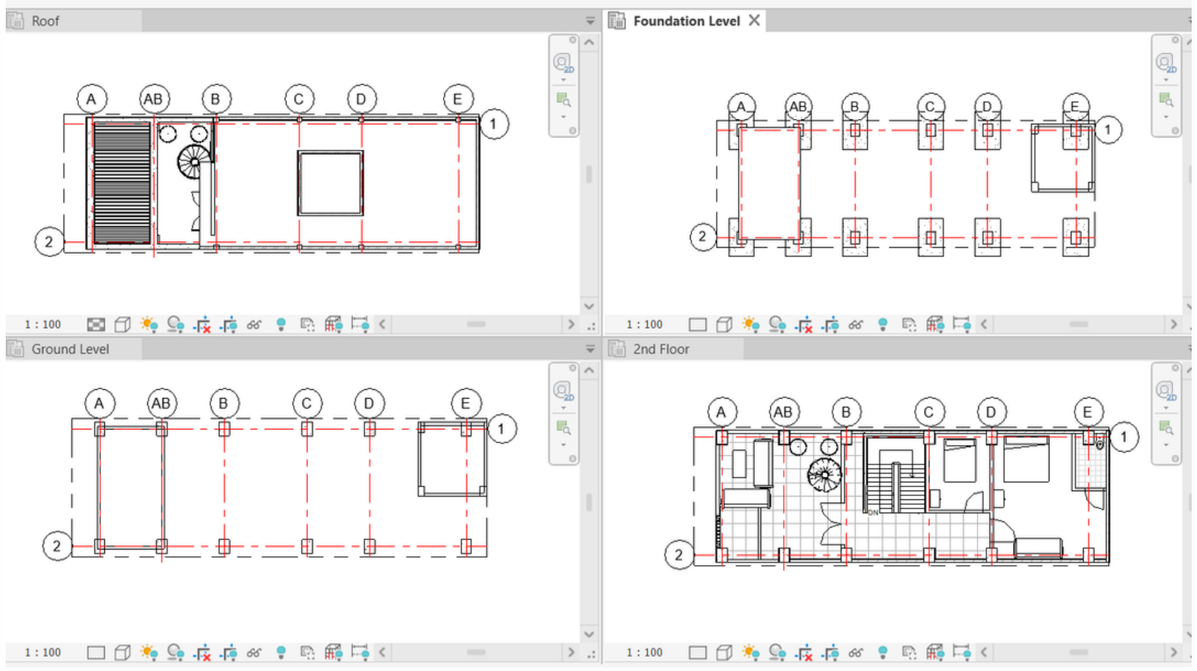
Roof
Foundation Level
Ground Level
2nd Floor
A
AB
B
C
D
E
1
2
1 : 100

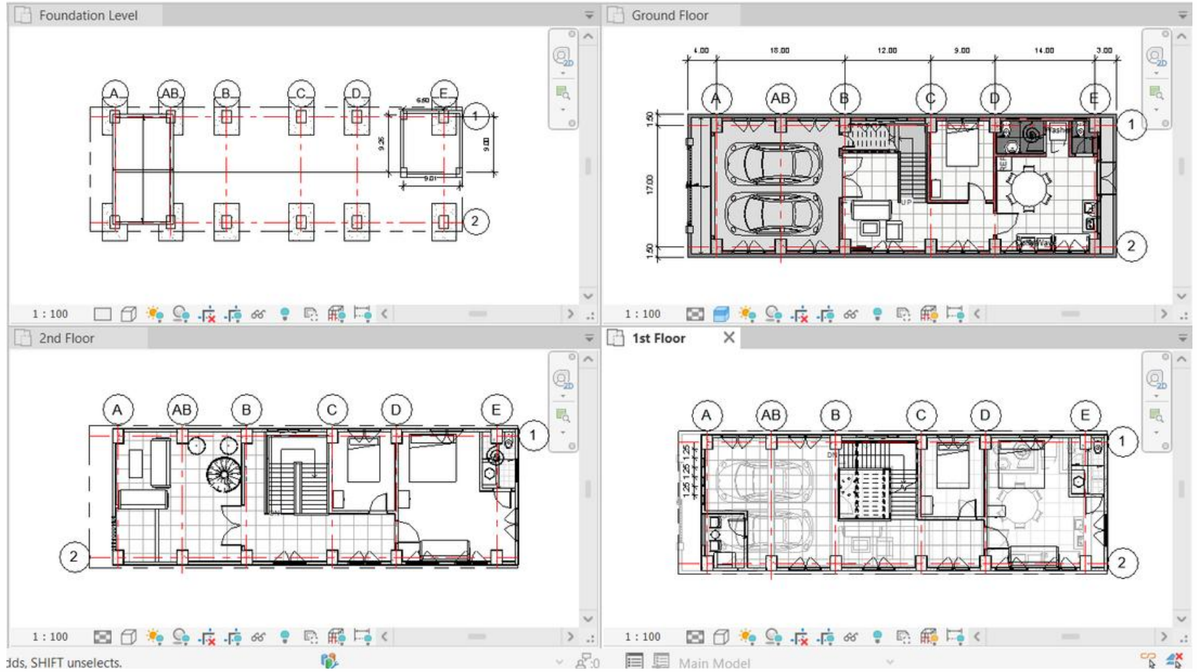
Foundation Level
Ground Floor
2nd Floor
1st Floor
A
AB
B
C
D
E
1
2
1 : 100
Main Model

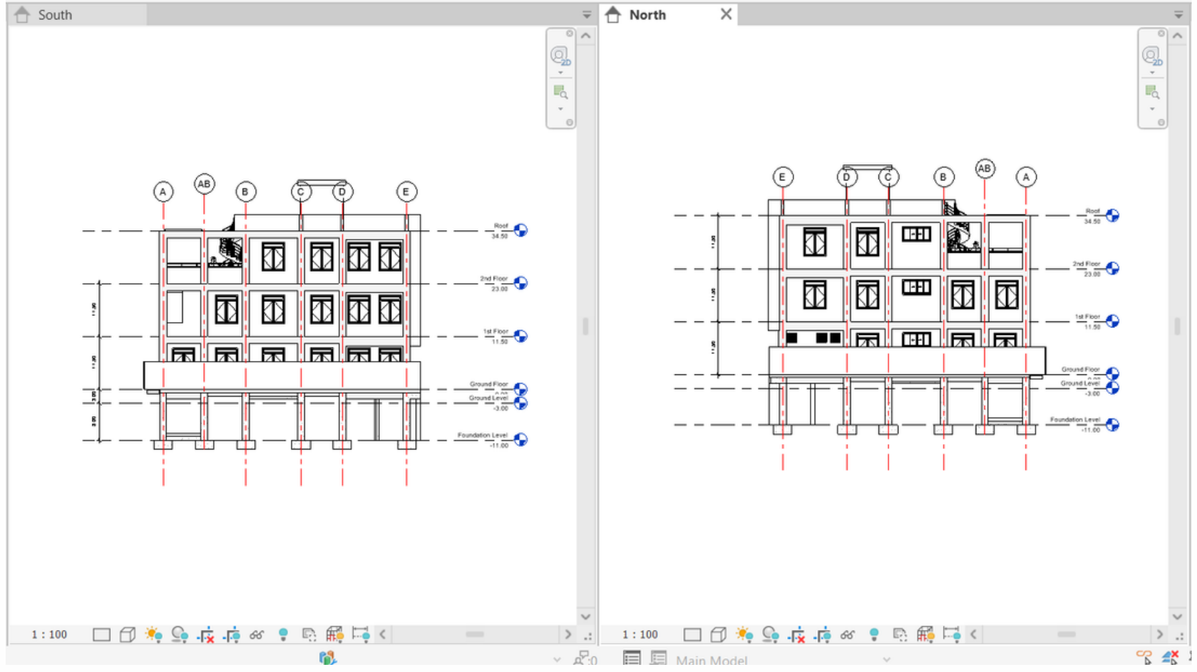
South
North
A
AB
B
C
D
E
Roof
34.50
2nd Floor
23.00
1st Floor
11.50
Ground Floor
0.00
Ground Level
-3.00
Foundation Level
-11.00
1 : 100
Main Model

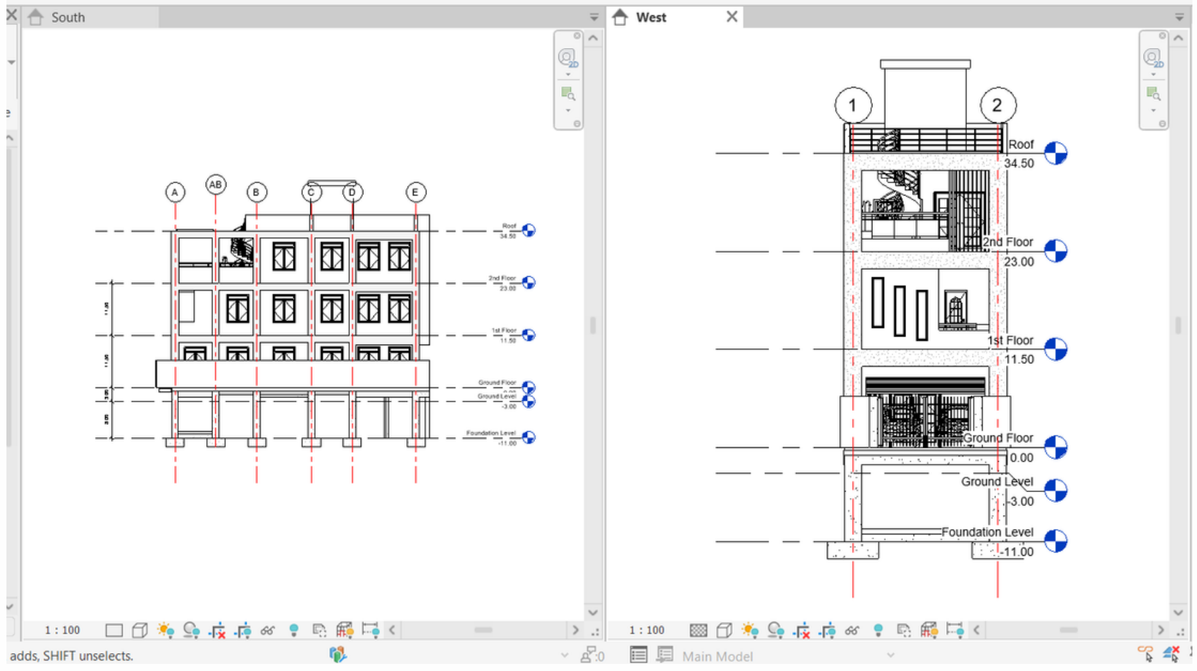
South
West
A
AB
B
C
D
E
1
2
Roof
34.50
2nd Floor
23.00
1st Floor
11.50
Ground Floor
0.00
Ground Level
-3.00
Foundation Level
-11.00
1 : 100
Main Model

Project 09

- Project : Mix Used Building Project
- Location: Myanmar
- Software: Autodesk Revit 2024
- Type: Residential





Garden



Swimming Pool




Entrance




Entrance




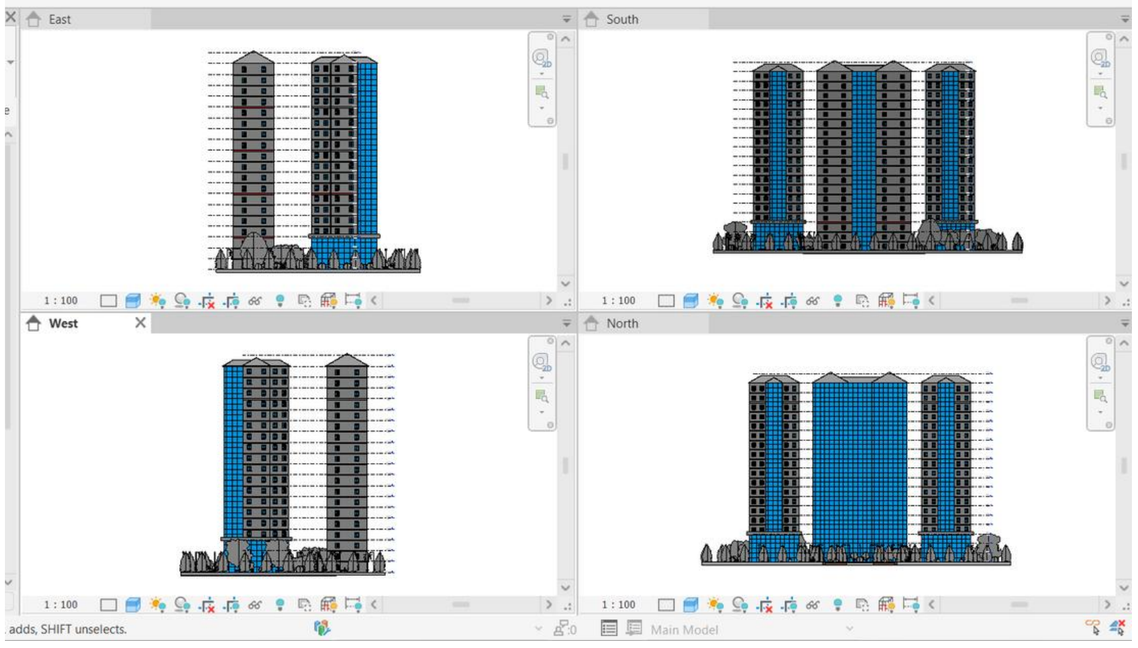



East
South
West
North
1 : 100
adds, SHIFT unselects.
Main Model

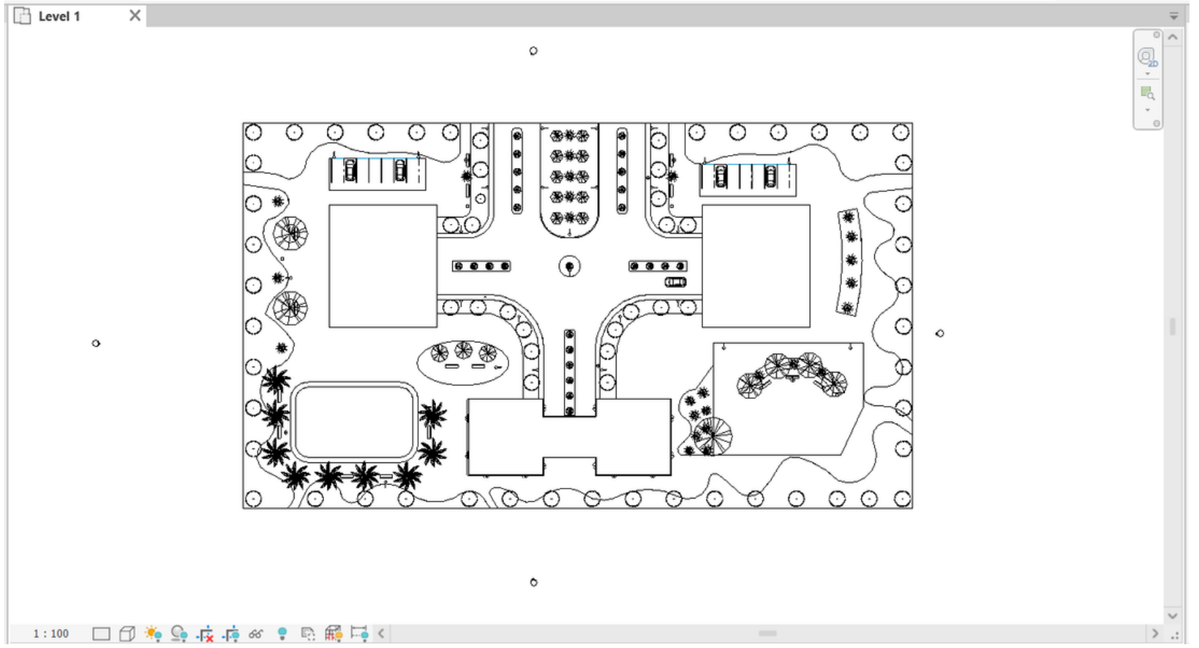
Level 1
1 : 100

Project 10

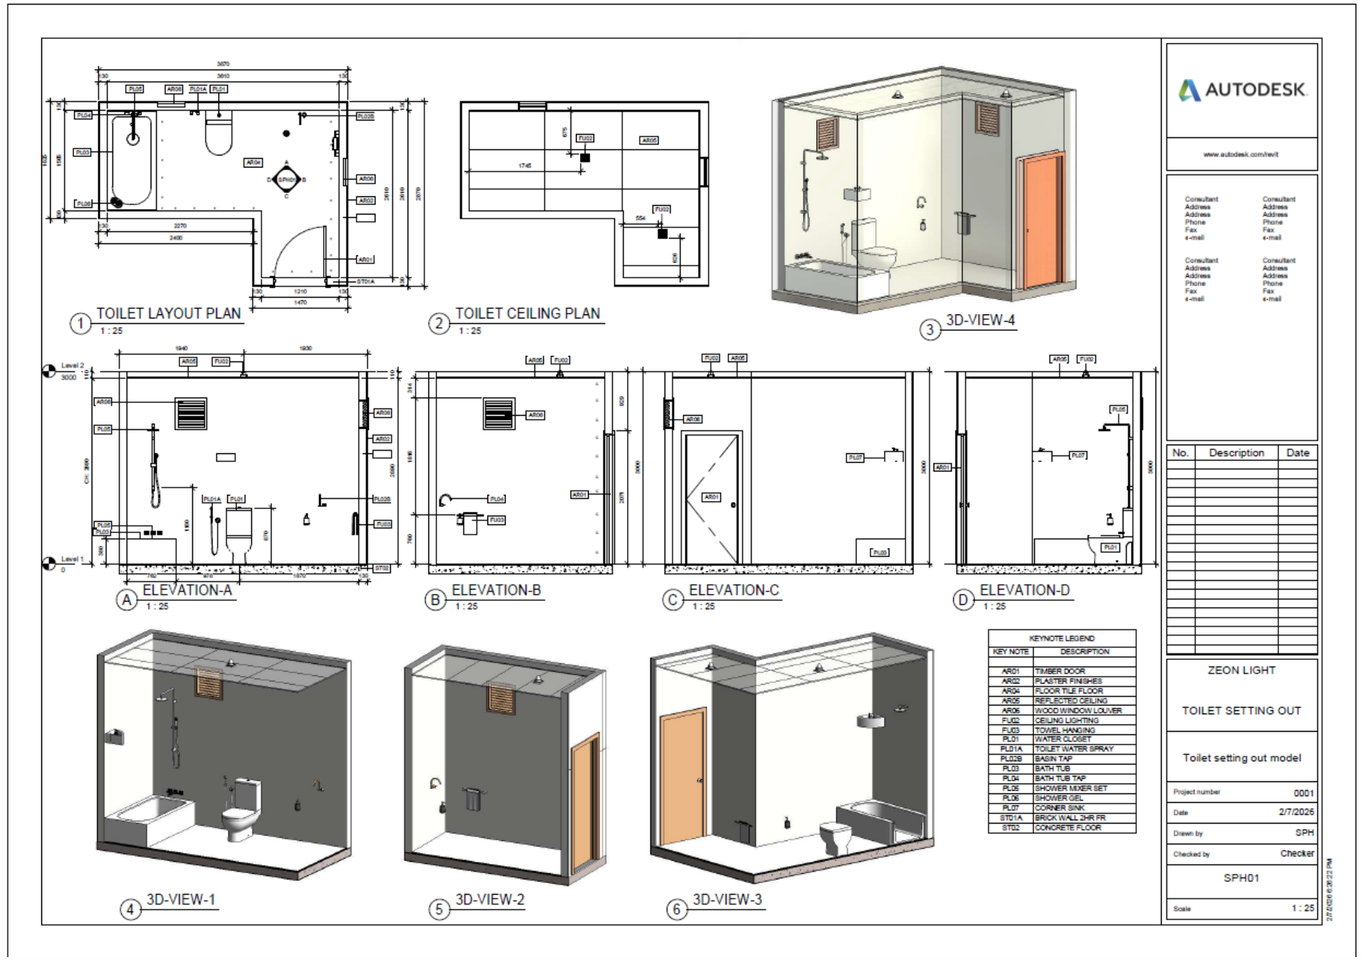


- Project : Toilet Setting Out
- Software: Autodesk Revit 2024

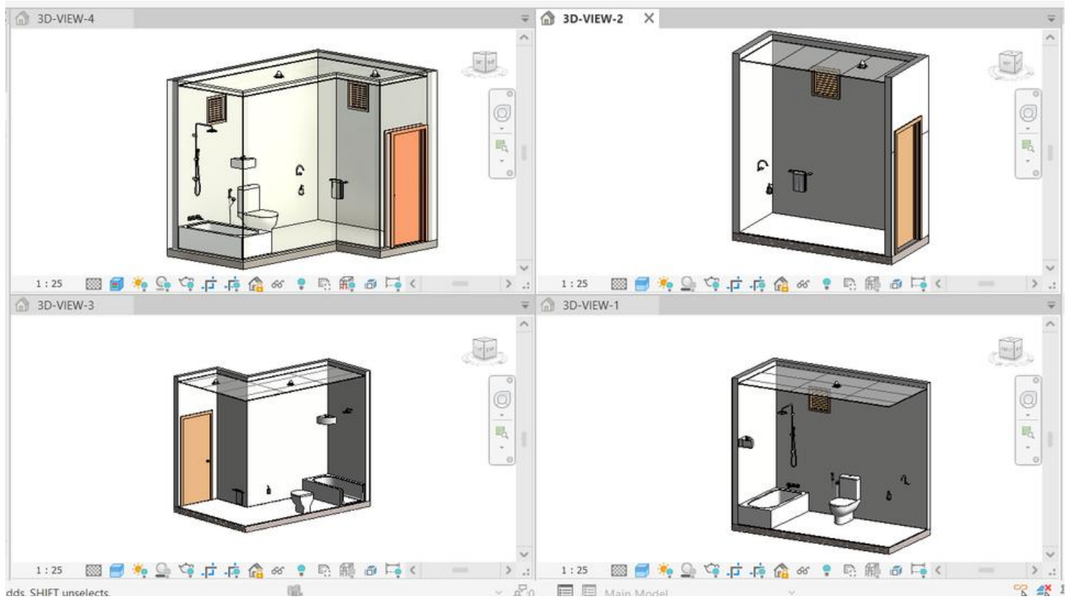






Project 11

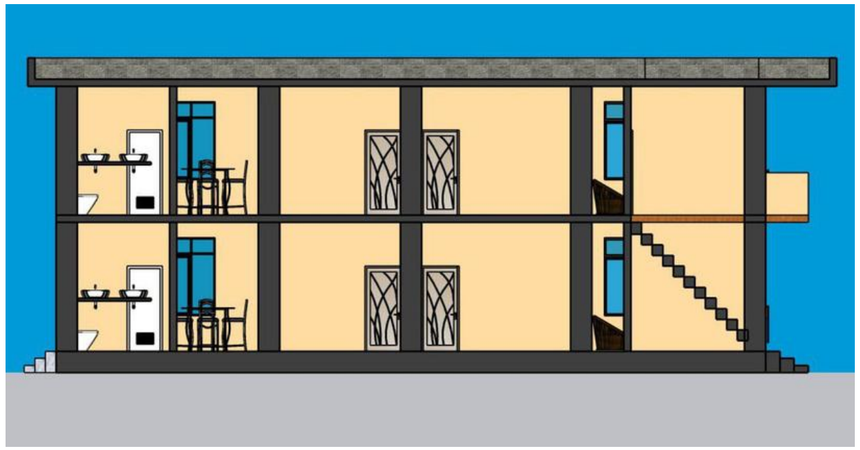

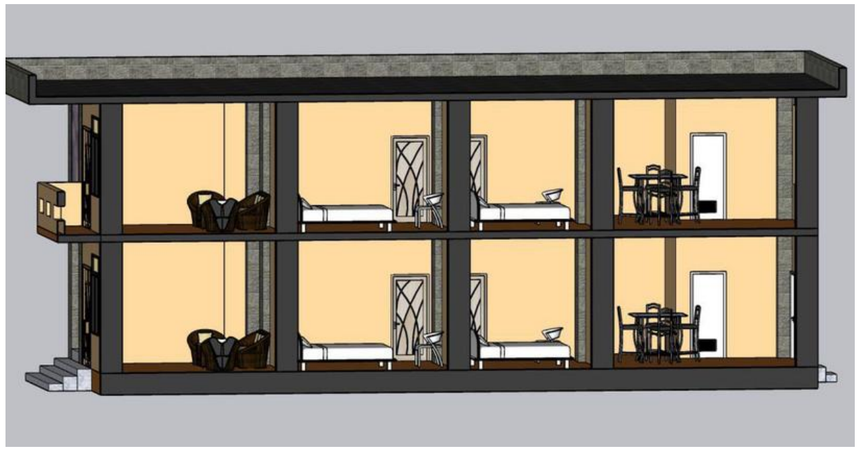



- Residential Design: Two Storey Building Project
- Project Type: Personal Project
- Location: Myanmar
- Software: Sketchup 2024
- Type: Residential







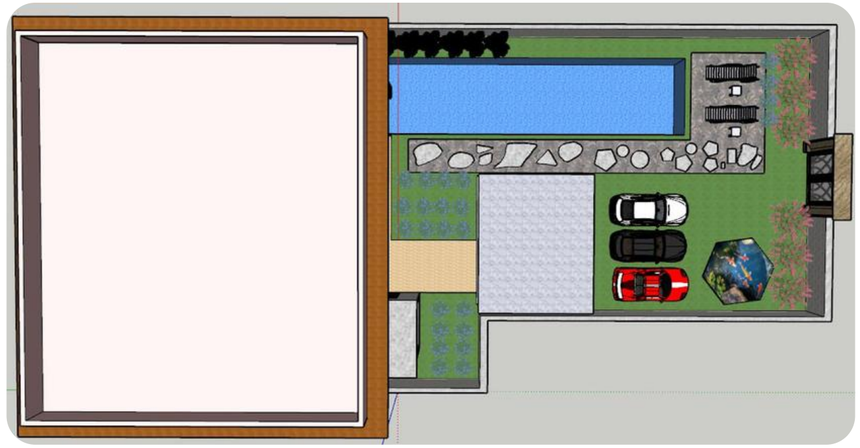

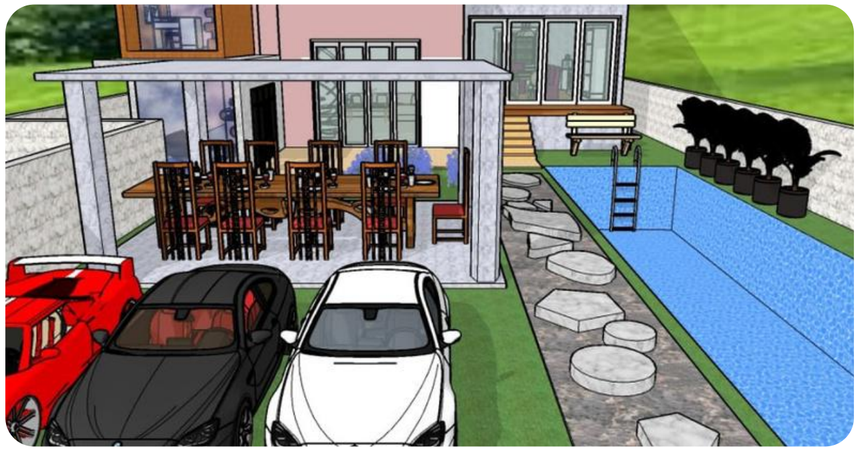







Project 12

- Design: Guest House – Exterior 3D Modelling
- Project Type: Academic Project
- Location: Myanmar
- Software: Sketchup 2024
- Type: Residential



Project 13

- Project name - Monastery
- Location: Myanmar
- Software: Sketchup 2024





14. Other Projects

- Software: SketchUp 2024
- Project: Interior Design










14. Other Projects

- Software: Tekla Structural Designer 2025
- Project Type: Training Project
- Scope: 3D Structural Modeling & Basic Structural Analysis

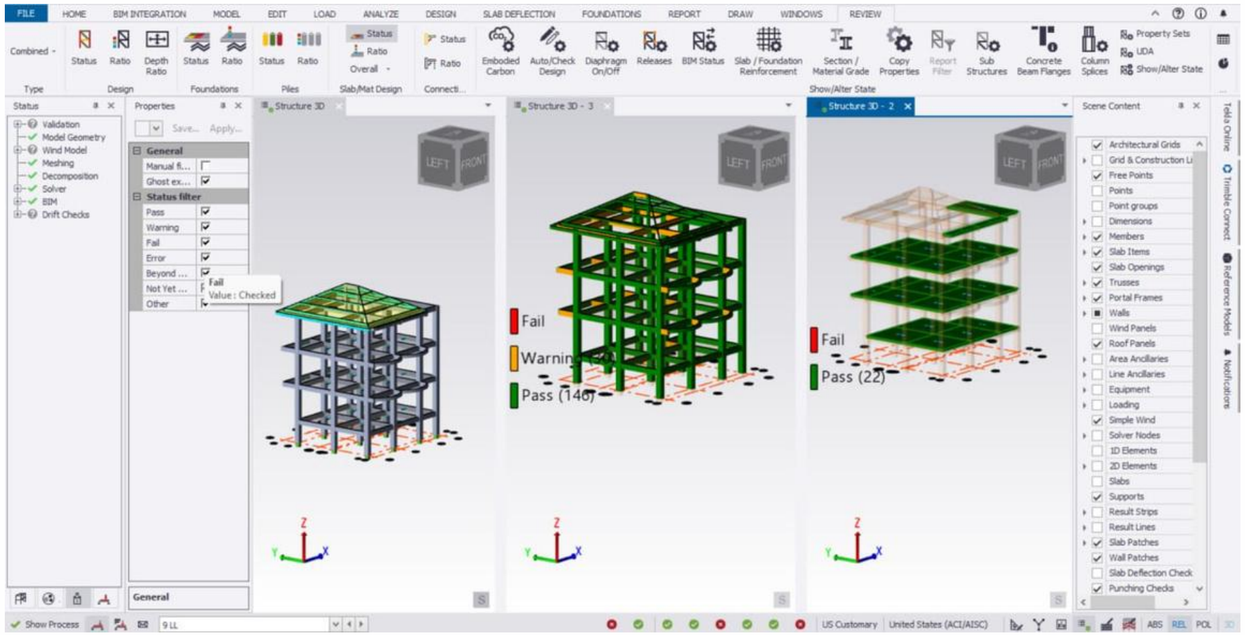

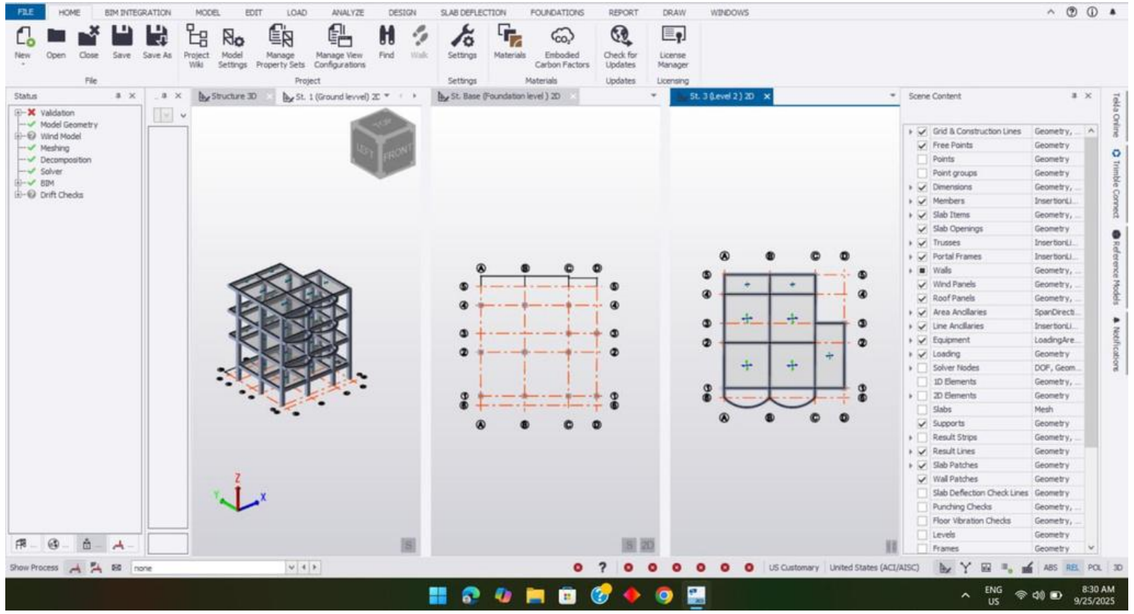

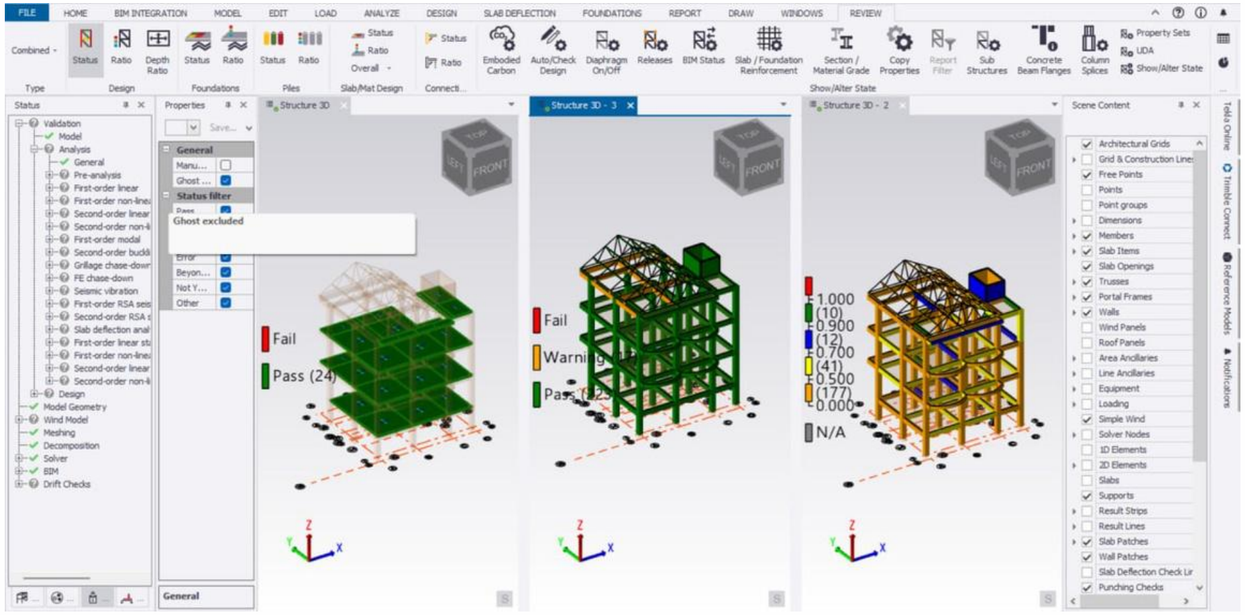

PROFESSIONAL DEVELOPMENT

CONTINUOUS LEARNING & SKILL DEVELOPMENT

01 / PROFESSIONAL TRAINING

1.BIM Level 01 – Architecture & Structure

- BIM Modeling (Architecture & Structure)
- Revit Family & Component Library Creation
- BIM Documentation & Data Extraction
- Collaboration Tools & Worksharing

1.BIM Level 02 – Advanced Architectural BIM

- Advanced Architectural BIM Modeling
- Conceptual & Parametric Modeling
- Dynamo Visual Programming
- Interior, Exterior & Landscape Modeling
- Visualization, Rendering & Documentation

1.Chinese (Mandarin)

- Speaking
- Listening

02 / CURRENTLY DEVELOPING SKILLS (SOFTWARE & TECHNICAL SKILLS)

AUTODESK Revit

AUTODESK Navisworks Manage

Dynamo

THANK YOU

FOR REVIEWING MY PORTFOLIO

Drafter | BIM Modeler

Architectural Drafting • BIM Modeling • 3D Visualization

BETTER DESIGNS FOR A BRIGHTER TOMORROW

SEIN PYAE HTAY

pyaepyae205200@gmail.com | +959 400523608 (Whatsapp) | https://www.linkedin.com/in/sein-pyae-htay