

# Portfolio

## Sein Pyae Htay

2026

# Hello,

I’m Sein Pyae Htay

Drafter cum BIM Modeler

Advanced Diploma in Civil Engineering

City and Gulids London Institute (UK)

+959 400523608 (Whatsapp)

pyaepyae205200@gmail.com

https://www.linkedin.com/in/sein-pyae-htay



# About Me

I am a Civil Engineering professional with approximately 3 years of experience in construction drafting, architectural documentation, and BIM modelling. I hold a Level 4 Diploma and Level 5 Advanced Diploma in Civil Engineering, with practical experience in both site engineering and technical drawing preparation.

I began my career as a Site Engineer cum Drafter and later progressed to BIM Modeler cum Drafter at King Construction. Throughout my professional experience, I have been involved in construction drawing preparation, site coordination, architectural drafting, 3D building modelling, and technical documentation.

My core technical expertise includes AutoCAD 2D Drafting and Autodesk Revit BIM Modelling, particularly in architectural and structural drawing development.

Through my experience, I have developed a good understanding of construction processes, drawing coordination, technical requirements, and project documentation. I am detail-oriented and responsible, with a strong commitment to producing accurate, high-quality technical drawings while continuously enhancing BIM capabilities and contributing to efficient construction and architectural projects.

# MY CERTIFICATES

## AutoCAD Intermediate



CERTIFICATE OF COMPLETION

**CONGRATULATIONS!**

You have successfully completed an Autodesk® Authorized Training Center® course specifically designed to satisfy your training requirements. Authorized Training Center instructors deliver quality–learning experiences with courses related to Autodesk products utilizing relevant content and comprehensive courseware. Autodesk's vision is to help people imagine, design, and create a better world.

Certificate No. AP702813098697555761782

| | | |
|---|---|---|
| MS SEIN PYAE HTAY | | |
| NAME | | |
| AUTOCAD (INTERMEDIATE) | | AUTOCAD 2025 |
| COURSE TITLE | | PRODUCT |
| HSU MYAT HMWE | 07-MARCH-2026 | 41-100 HOURS |
| INSTRUCTOR | COURSE DATE | COURSE DURATION |

ZEON LIGHT TRAINING CENTRE
AUTODESK AUTHORIZED TRAINING CENTER

AUTODESK
Authorized Training Center

Autodesk, the Autodesk logo, and ATC are registered trademarks or trademarks of Autodesk, Inc., and/or its subsidiaries and/or affiliates in the USA and/or other countries. All other brand names, product names, or trademarks belong to their respective holders. Autodesk reserves the right to alter product and services offerings, and specifications and pricing at any time without notice, and is not responsible for typographical or graphical errors that may appear in this document. Autodesk did not provide this training course or any of the training materials. The Autodesk Learning Partner provided all course materials and training. © 2026 Autodesk, Inc. All rights reserved.

## Professional Civil Engineering Completion Certificate



# MY CERTIFICATES

## Revit Architecture & Structure Essentail



## CERTIFICATE OF COMPLETION

**CONGRATULATIONS!**

You have successfully completed an Autodesk® Authorized Training Center® course specifically designed to satisfy your training requirements. Authorized Training Center instructors deliver quality-learning experiences with courses related to Autodesk products utilizing relevant content and comprehensive courseware. Autodesk's vision is to help people imagine, design, and create a better world.

Certificate No. AP702813098658015761782

| | | |
|---|---|---|
| MS SEIN PYAE HTAY | | |
| NAME | | |
| REVIT ARCHITECTURE & STRUCTURE ESSENTIAL | | REVIT 2025 |
| COURSE TITLE | | PRODUCT |
| PYAE PHYO ZAW | 09-FEBRUARY-2026 | 41-100 HOURS |
| INSTRUCTOR | COURSE DATE | COURSE DURATION |

ZEON LIGHT TRAINING CENTRE
AUTODESK AUTHORIZED TRAINING CENTER

AUTODESK
Authorized Training Center


Autodesk, the Autodesk logo, and ATC are registered trademarks or trademarks of Autodesk, Inc., and/or its subsidiaries and/or affiliates in the USA and/or other countries. All other brand names, product names, or trademarks belong to their respective holders. Autodesk reserves the right to alter product and services offerings, and specifications and pricing at any time without notice, and is not responsible for typographical or graphical errors that may appear in this document. Autodesk did not provide this training course or any of the training materials. The Autodesk Learning Partner provided all course materials and training. © 2026 Autodesk, Inc. All rights reserved.

## Professional Civil Engineering Achievement Certificate (2nd Award)



# MY CERTIFICATES

## SketchUp Certificate

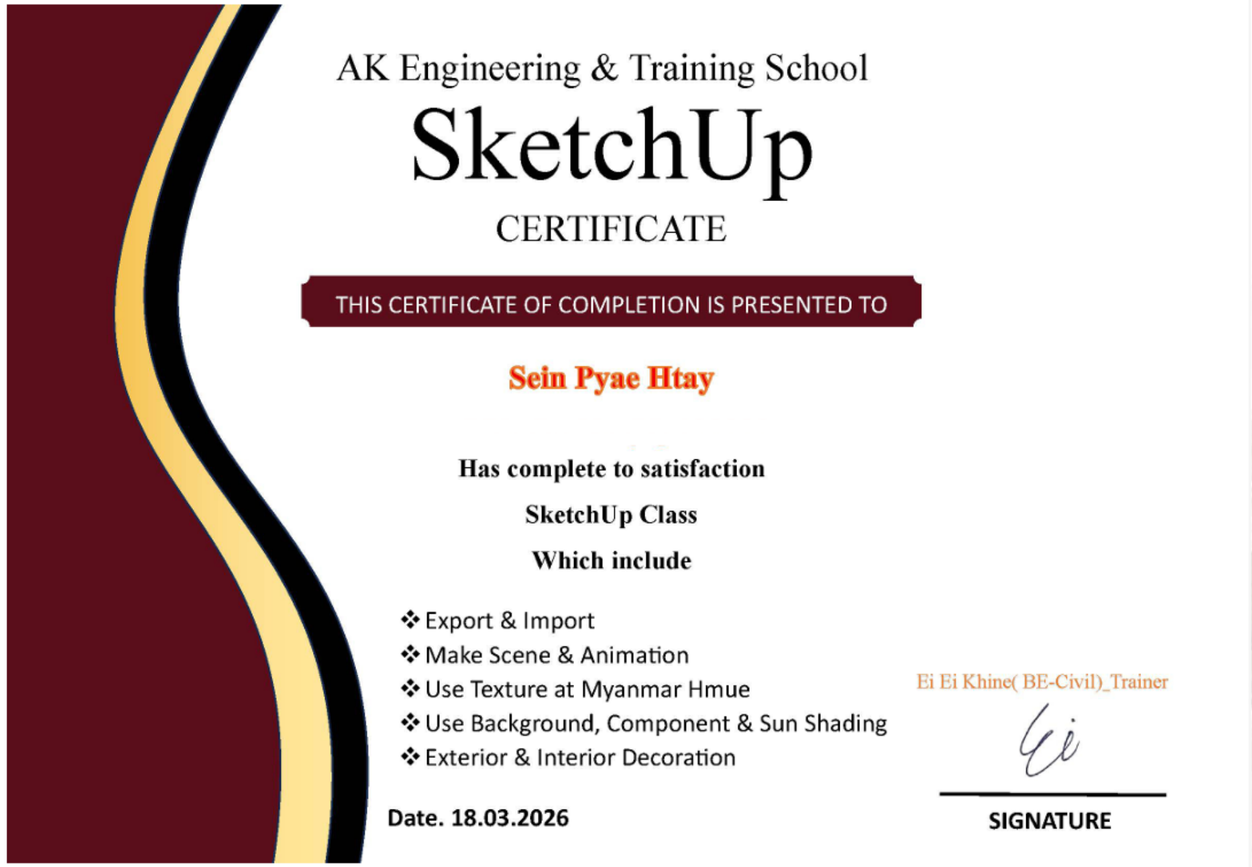

AK Engineering & Training School

SketchUp

CERTIFICATE

THIS CERTIFICATE OF COMPLETION IS PRESENTED TO

**Sein Pyae Htay**

**Has complete to satisfaction**

**SketchUp Class**

**Which include**

- Export & Import
- Make Scene & Animation
- Use Texture at Myanmar Hmue
- Use Background, Component & Sun Shading
- Exterior & Interior Decoration

**Date. 18.03.2026**

Ei Ei Khine( BE-Civil)_Trainer

**SIGNATURE**

## Professional Graphic Design Certificate



GCTI

Certificate of Training

This certificate is proudly presented to

Sein Pyae Htay

for successfully completing the

Professional Graphic Design Course

at GENESYS COMPUTER & TECHNOLOGY INSTITUTE

Given on the 15th day of December 2023

A

GRADE

GENESYS COMPUTER & TECHNOLOGY INSTITUTE Reg No:126076886

Head of Instructors and President of GCTI

# Education

## City & Gulids London Institute 2023 - 2026

- Level 5 - Advanced Diploma in Civil Engineering (Distinction) (2025 - 2026)
- Level 4 - Diploma in Civil Engineering (2024 - 2025)
- Level 3 - Diploma in Civil Engineering & Foundation (2023 - 2024)

## University Of the People 2024 - 2026

- Associate Degree in Business Administration (High honrs)

## Language

- English (Intermediate)
- Chinese ( Basic & Continue Learning)
- Burmese ( Native)

## Software Proficiency

- AutoCAD 
- Revit 
- Sketchup 
- Tekla 
- Adobe Photoshop 
- Microsoft Project 
- Microsoft Office ( Word, Excel, Powerpoint)
- Canva 

# Software Proficiency

## AutoCAD – Intermediate

- 2D architectural drafting
- Floor plans, elevations and sections
- Layers, dimensions and annotations
- Blocks and drawing organization
- Layout setup and plotting
- Drawing revisions

## Autodesk Revit – Basic to Intermediate

- 3D architectural modelling
- Walls, floors, roofs and ceilings
- Doors and windows
- Stairs and building components
- Floor plans, elevations and sections
- Sheet creation and documentation
- Basic family modification and creation

## Other Softwares

- SketchUp – 3D modelling
- Tekla - Basic knowledge of structural modelling
- Adobe Photoshop – Basic image editing
- Microsoft Project - Project scheduling, task tracking and Gantt charts
- Microsoft Excel – Documentation and spreadsheets
- Microsoft Word – Technical documentation
- Microsoft PowerPoint – Presentations
- Canva – Presentation design

# Selected Projects

- This portfolio showcases a selection of my personal, professional, and freelance projects, highlighting my skills in architectural drafting, BIM modelling, and 3D visualization.
- The main focus is on architectural drawings developed using Autodesk AutoCAD 2024, BIM projects created with Autodesk Revit 2024, and 3D modelling and visualization projects using SketchUp 2024, covering residential, commercial, hotel, interior, and exterior designs.

Portfolio Overview

1. Three Storey RCC Residential Building
   Autodesk AutoCAD 2024
2. Three and Half Storey Residential Building
   Autodesk AutoCAD 2024
3. One Storey RCC Building
   Autodesk AutoCAD 2024
4. Three and Half Storey Residential Building ISO Drawing
   Autodesk AutoCAD 2024
5. Three Storey with Penthouse Building Project
   Autodesk AutoCAD 2024
6. Three Storey RCC Residential Building
   Autodesk AutoCAD 2024
7. Five Storey Hotel Project
   Autodesk AutoCAD 2024

Portfolio Overview

8. Three and Half Stories Residential Building
   Autodesk Revit 2024
9. Mix Used Building Project
   Autodesk Revit 2024
10. Toilet Setting Out Model
    Autodesk Revit 2024
11. Two Storey Building Project
    Sketchup 2024
12. Guest House – Exterior 3D Modelling
    Sketchup 2024
13. Monastery Project
    Sketchup 2024
14. Other Projects
    Sketchup 2024 & Tekla Structural Designer

# Project 01

- Residential Design:  Three Storey RCC Building
- Location:Yangon, Myanmar
- Software: AutoCAD & SketchUp 2024
- Type: Residential



- Project - Residential Building 3D Model
- Scope - Exterior 3D Modeling
- Software - Sketchup 2024













- Drawings - Layout Plan, Detail Drawing & Elevation
- Software - Autodesk AutoCAD 2024

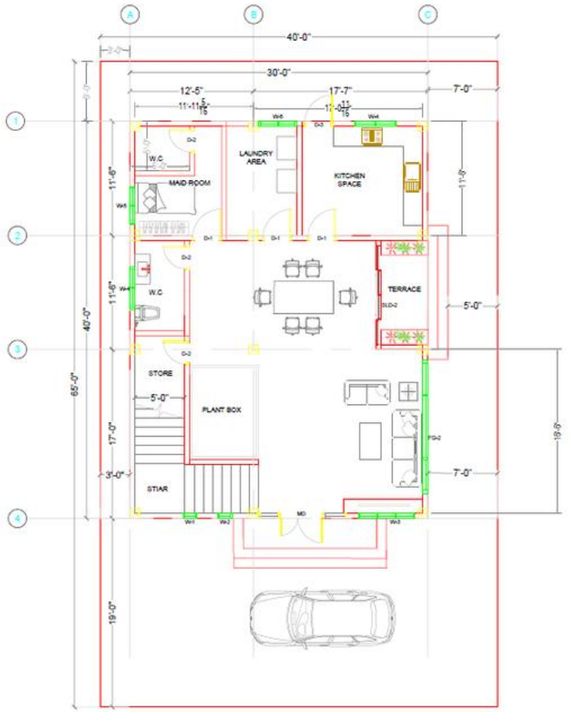



BUILDING LAYOUT PLAN

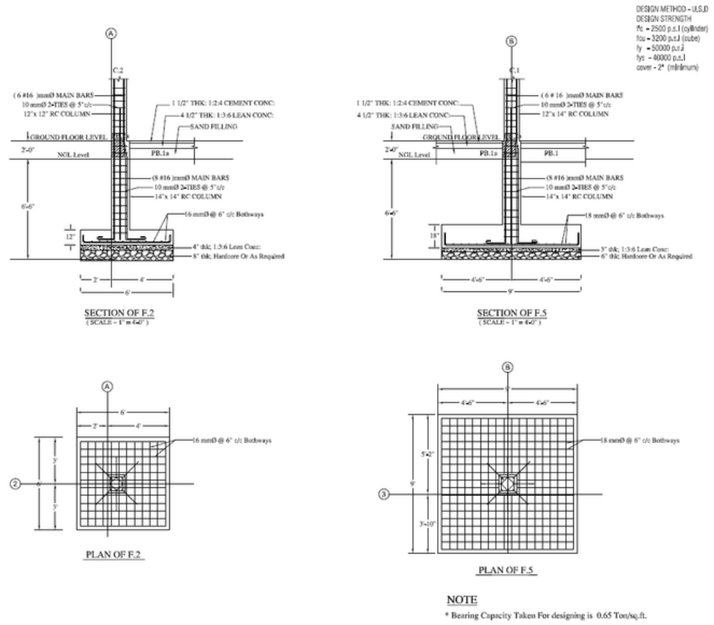

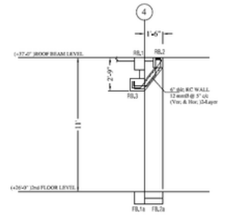


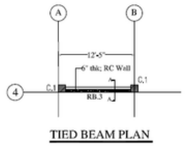
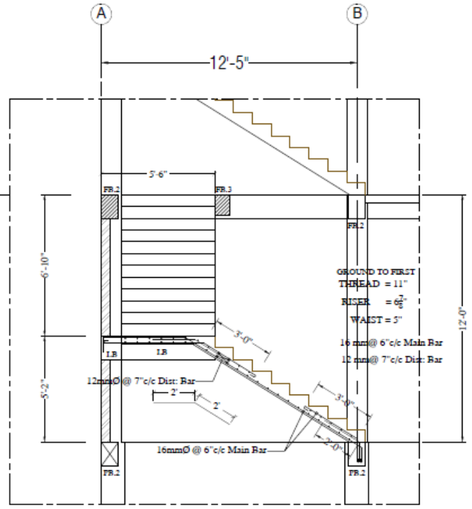


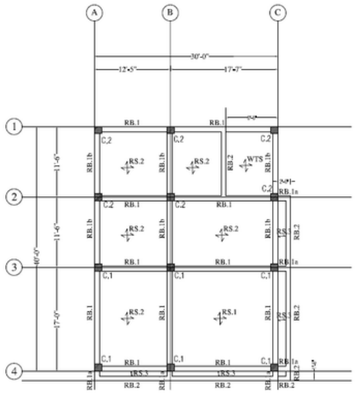





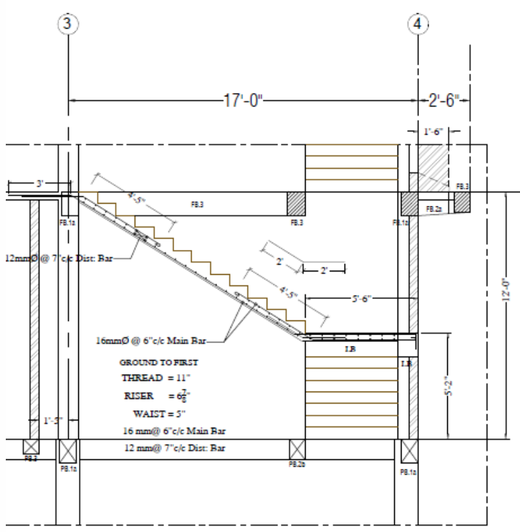

STAIR DETAIL




# Project 2


- Residential Design: Three and Half Storey Residential Building
- Location:Yangon, Myanmar
- Software: AutoCAD & SketchUp 2024
- Type: Residential







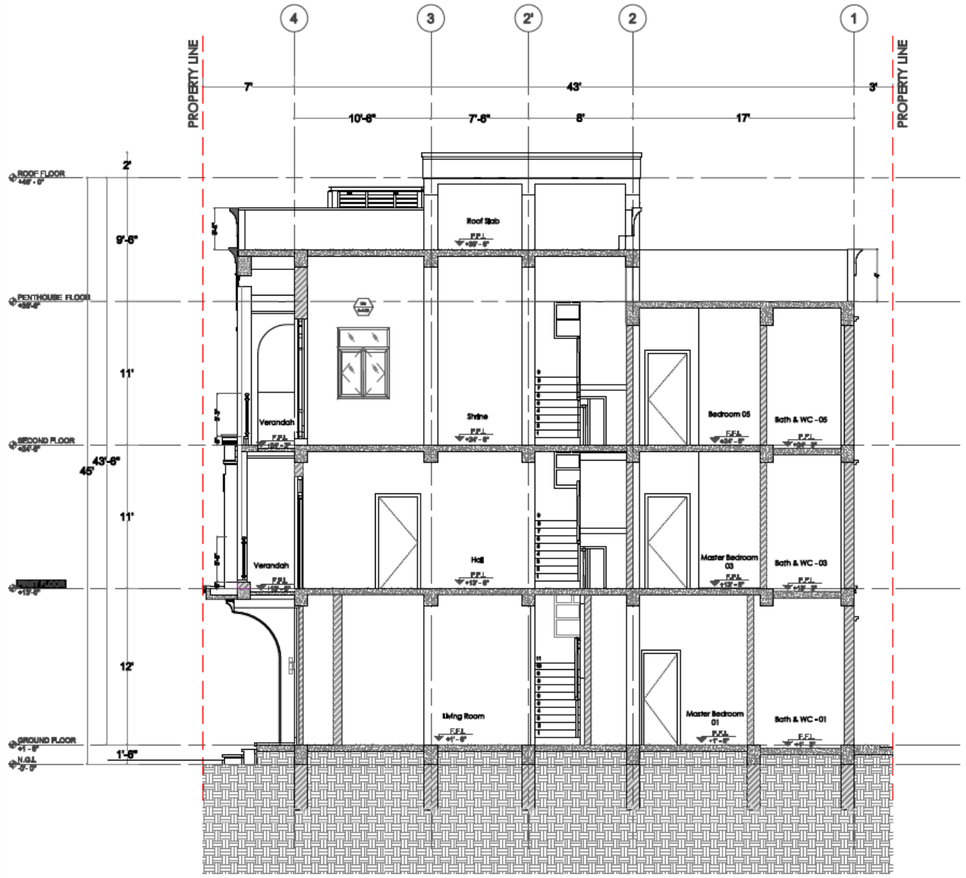


- Drawings - Plan, Detail Drawing, Section & Elevation
- Software - Autodesk AutoCAD 2024

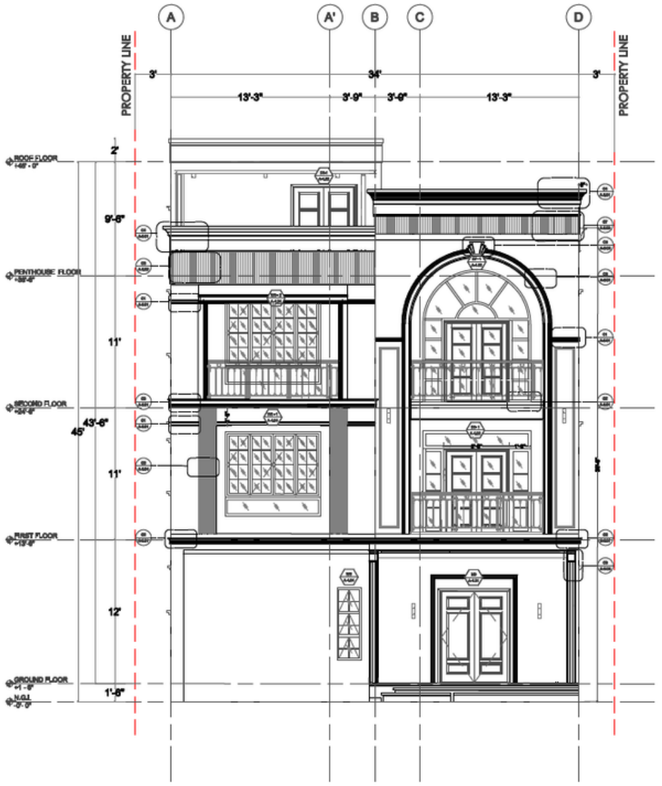

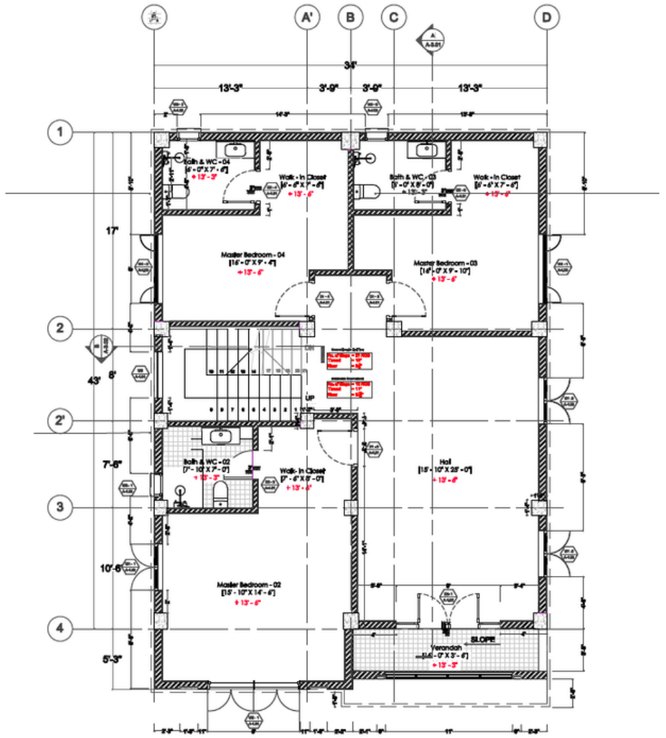


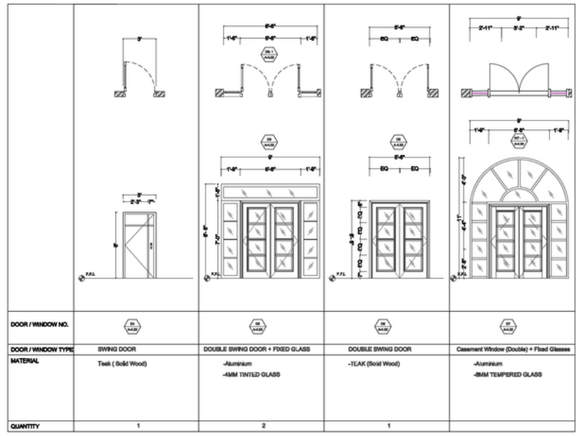
# Project 3







- Residential Design:  One Storey RCC Building
- Location: Toon Tay, Myanmar
- Software: AutoCAD & SketchUp 2024
- Type: Residential

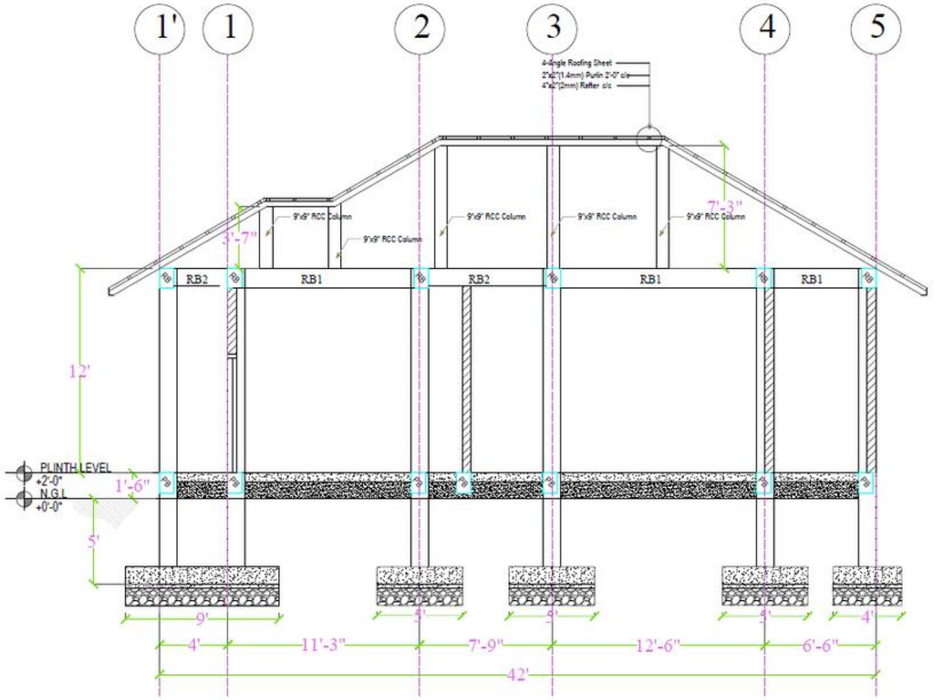



CROSS-SECTION

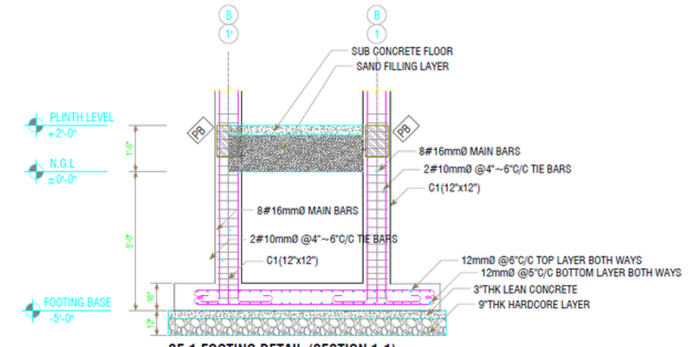


CF-1 FOOTING DETAIL (SECTION 1-1)

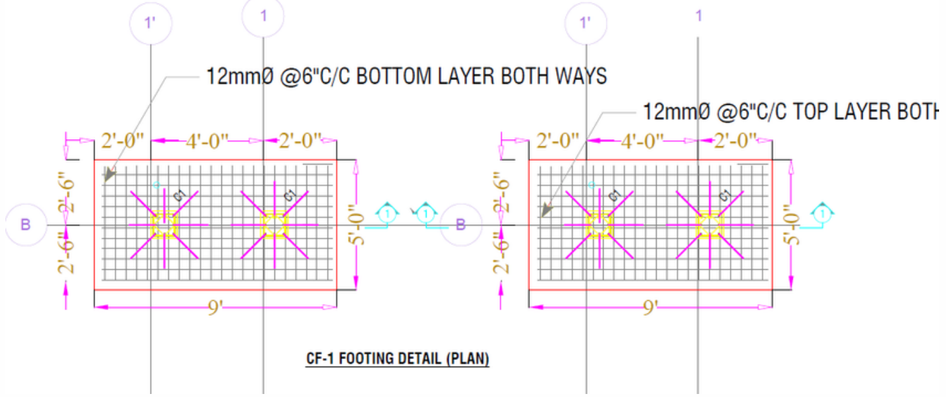


CF-1 FOOTING DETAIL (PLAN)

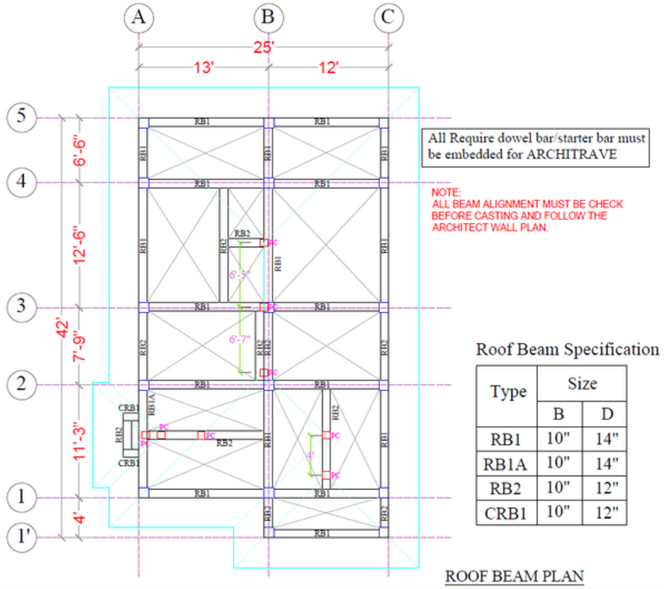


All Require dowel bar/starter bar must be embedded for ARCHITRAVE













NOTE:
ALL BEAM ALIGNMENT MUST BE CHECK BEFORE CASTING AND FOLLOW THE ARCHITECT WALL PLAN.

Roof Beam Specification

| Type | Size | |
|---|---|---|
| | B | D |
| RB1 | 10" | 14" |
| RB1A | 10" | 14" |
| RB2 | 10" | 12" |
| CRB1 | 10" | 12" |

ROOF BEAM PLAN

PLINTH BEAM SECTIONS
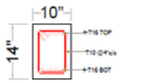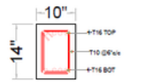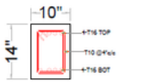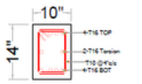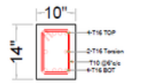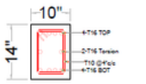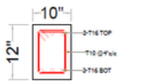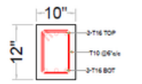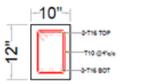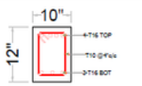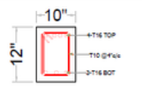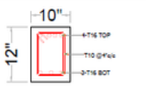
| LEFT | MID | RIGHT |
|---|---|---|
|  |  |  |
| PB-1 | PB-1 | PB-1 |
|  |  |  |
| PB-1A | PB-1A | PB-1A |
|  |  |  |
| PB-2 | PB-2 | PB-2 |
|  |  |  |
| CPB-1 | CPB-1 | CPB-1 |


# Project 4

- Residential Design: Three and Half Storey Residential Building
- Location:Yangon, Myanmar
- Software: AutoCAD 2024
- Type: Residential








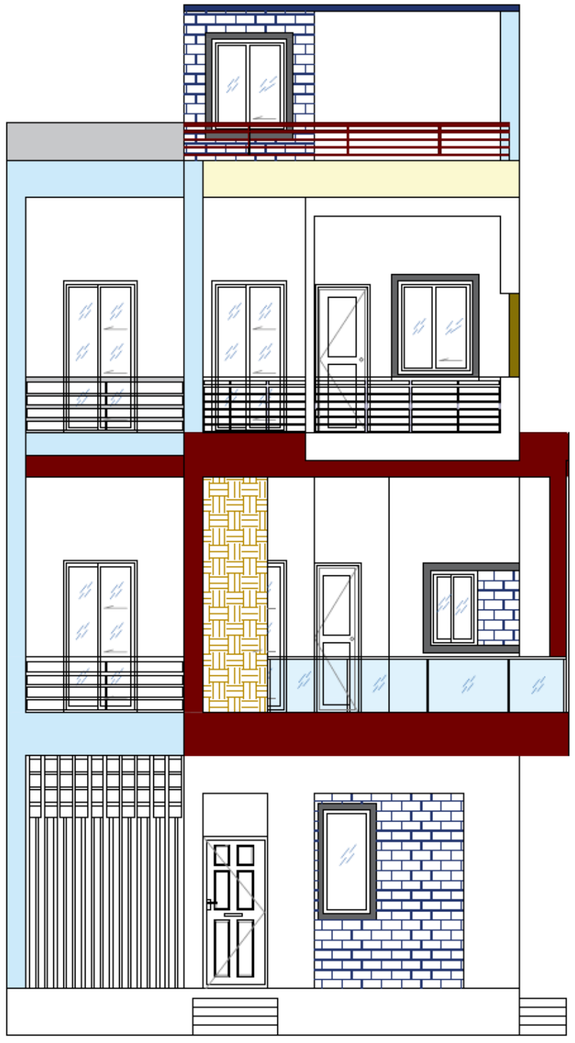


Front Elevation View

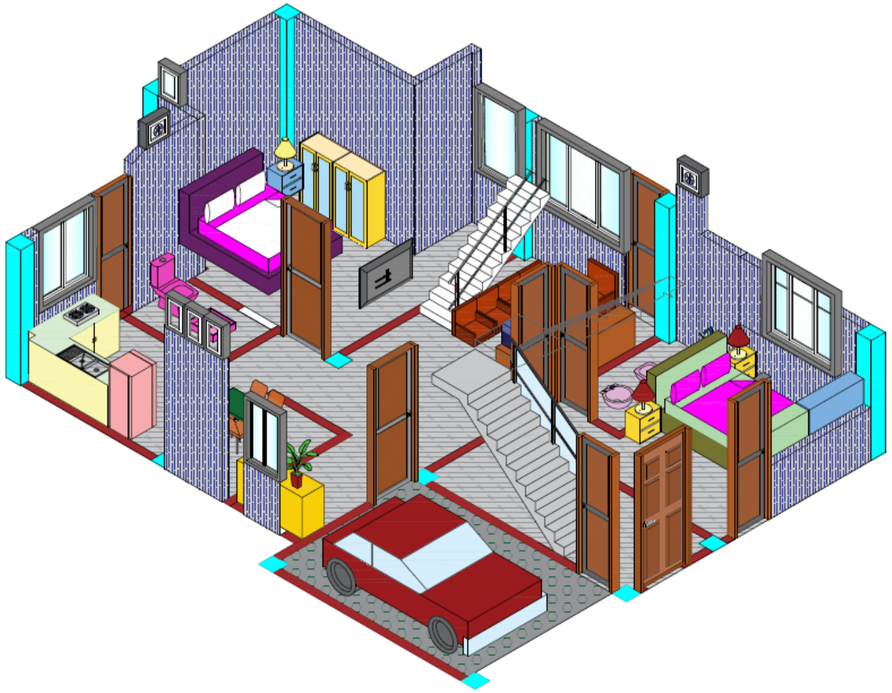



Door and Window Details

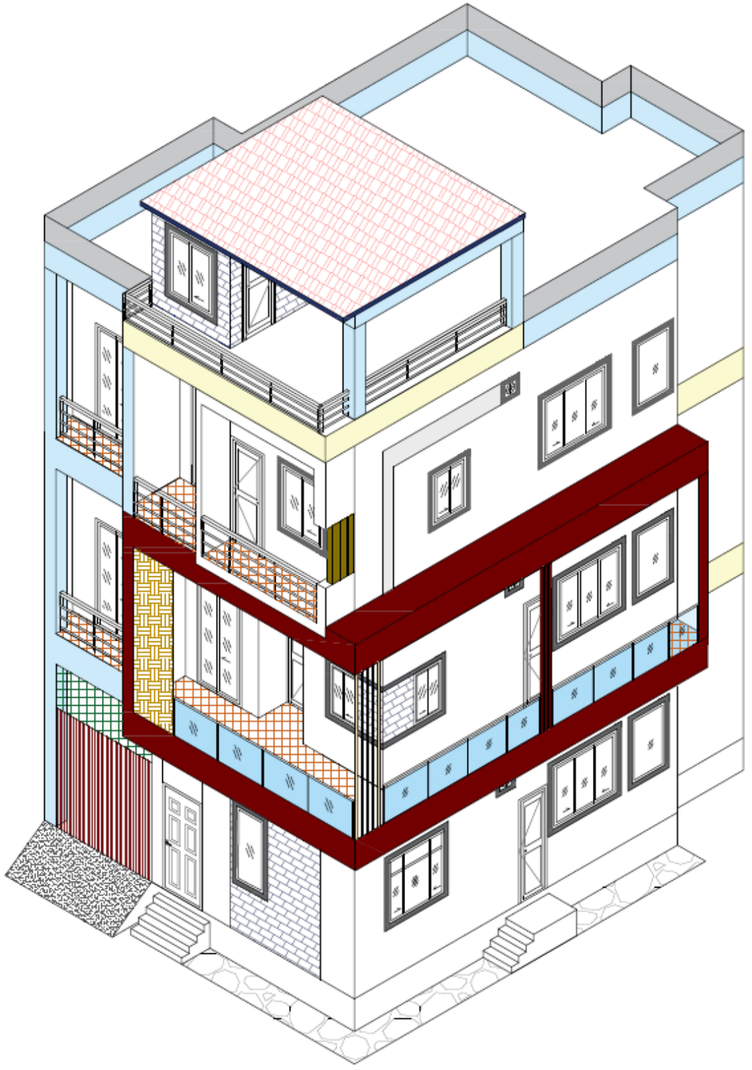



ISOMETRIC VIEW






# Project 05


- Residential Design: Three Storey with Penthouse Building Project
- Location: Yangon, Myanmar
- Software: AutoCAD 2024
- Type: Residential

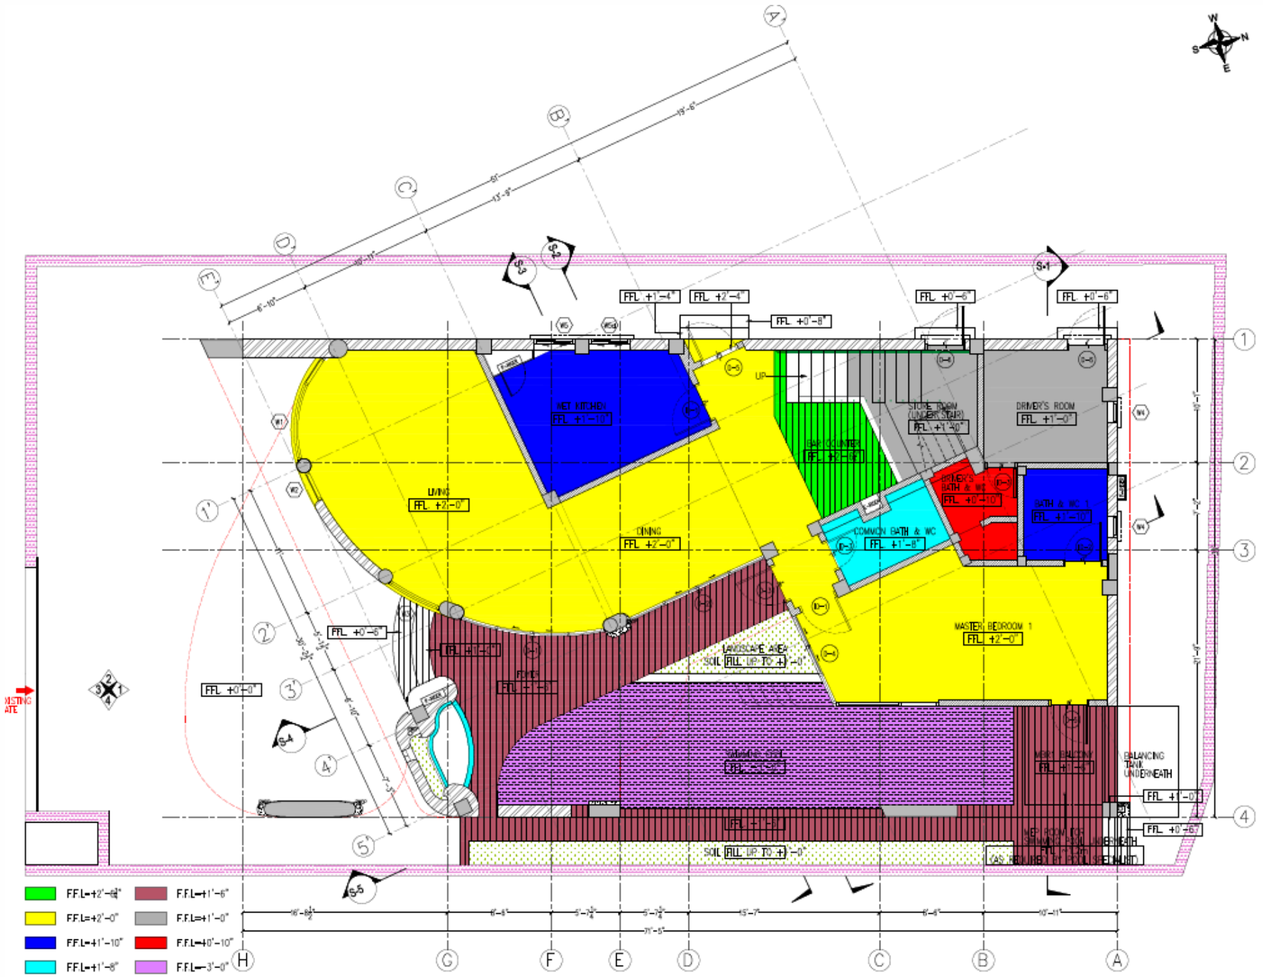

WET KITCHEN
FFL +1'-10"
LIVING
FFL +2'-0"
DINING
FFL +2'-0"
BAR COUNTER
FFL +2'-4"
TOILET ROOM (UNDER STAIR)
FFL +1'-10"
DRIVER'S ROOM
FFL +1'-0"
PROJECTED BATH & WC
FFL +0'-10"
COMMON BATH & WC
FFL +1'-8"
BATH & WC 1
FFL +1'-10"
MASTER BEDROOM 1
FFL +2'-0"
LANDSCAPE AREA
SOIL FILL UP TO +0'-0"
FFL +0'-6"
FFL +0'-0"
MOTOR HOUSE
FFL +1'-0"
SUMP
FFL -3'-0"
BALANCING TANK UNDERNEATH
SOIL FILL UP TO +0'-0"
MEETING GATE
F.F.L=+2'-4"
F.F.L=+2'-0"
F.F.L=+1'-10"
F.F.L=+1'-8"
F.F.L=+1'-6"
F.F.L=+1'-0"
F.F.L=+0'-10"
F.F.L=-3'-0"

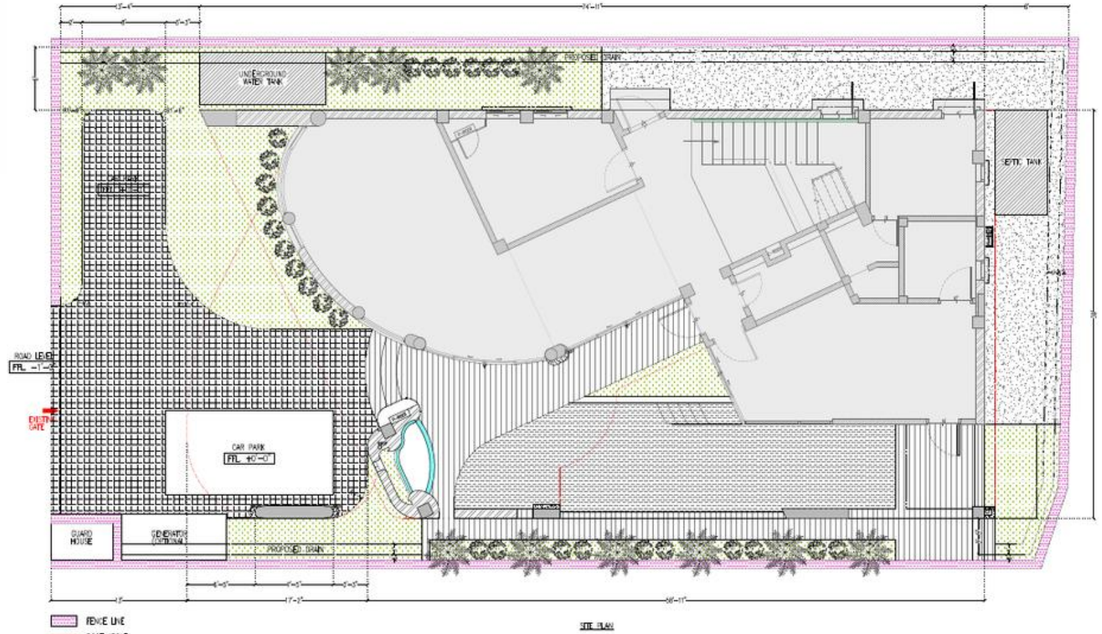

UNDERGROUND WATER TANK
SEPTIC TANK
ROAD LEVEL
FFL -1'-3"
EXISTING GATE
CAR PARK
FFL +0'-0"
GUARD HOUSE
GENERATOR (OPTIONAL)
PROPOSED DRAIN
FENCE LINE
ROOF ABOVE
GRASS
CONCRETE FLOORING
OUTDOOR TILE
SITE PLAN

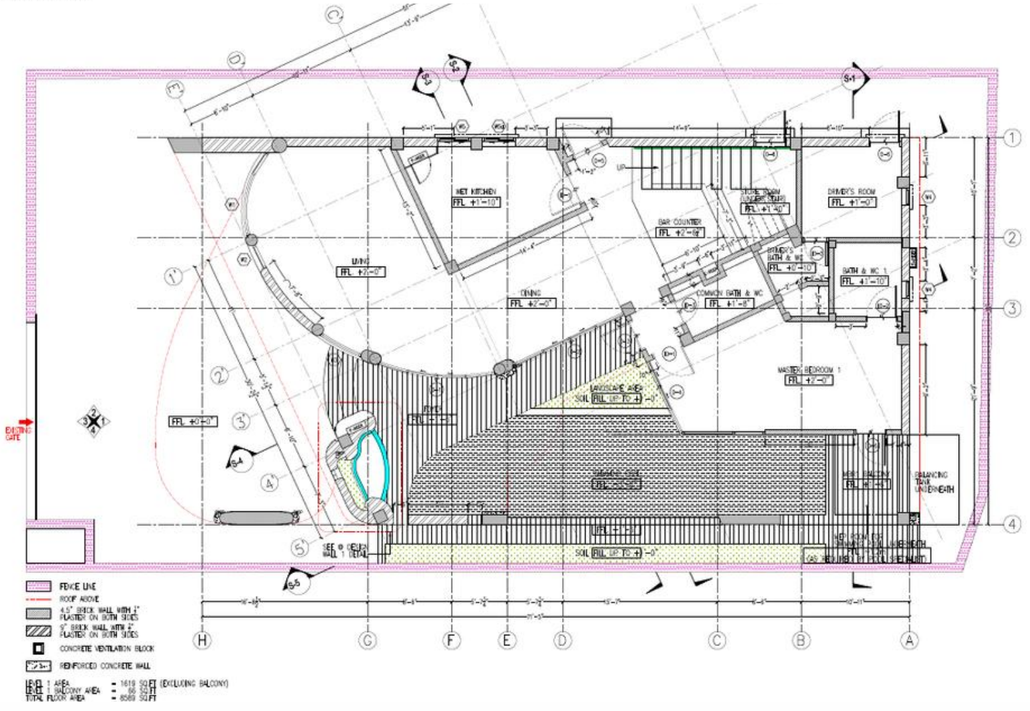
WET KITCHEN
FFL +1'-10"
LIVING
FFL +2'-0"
DINING
FFL +2'-0"
BAR COUNTER
FFL +2'-4"
TOILET ROOM (UNDER STAIR)
FFL +1'-10"
DRIVER'S ROOM
FFL +1'-0"
PROJECTED BATH & WC
FFL +0'-10"
COMMON BATH & WC
FFL +1'-8"
BATH & WC 1
FFL +1'-10"
MASTER BEDROOM 1
FFL +2'-0"
LANDSCAPE AREA
SOIL FILL UP TO +0'-0"
FFL +0'-0"
SUMP
FFL -3'-0"
MOTOR HOUSE
FFL +1'-0"
BALANCING TANK UNDERNEATH
SOIL FILL UP TO +0'-0"
EXISTING GATE
FENCE LINE
ROOF ABOVE
9" BRICK WALL WITH 1" PLASTER ON BOTH SIDES
5" BRICK WALL WITH 1" PLASTER ON BOTH SIDES
CONCRETE VENTILATION BLOCK
REINFORCED CONCRETE WALL
LEVEL 1 AREA = 1618 SQ.FT (EXCLUDING BALCONY)
LEVEL 1 BALCONY AREA = 66 SQ.FT
TOTAL FLOOR AREA = 8589 SQ.FT

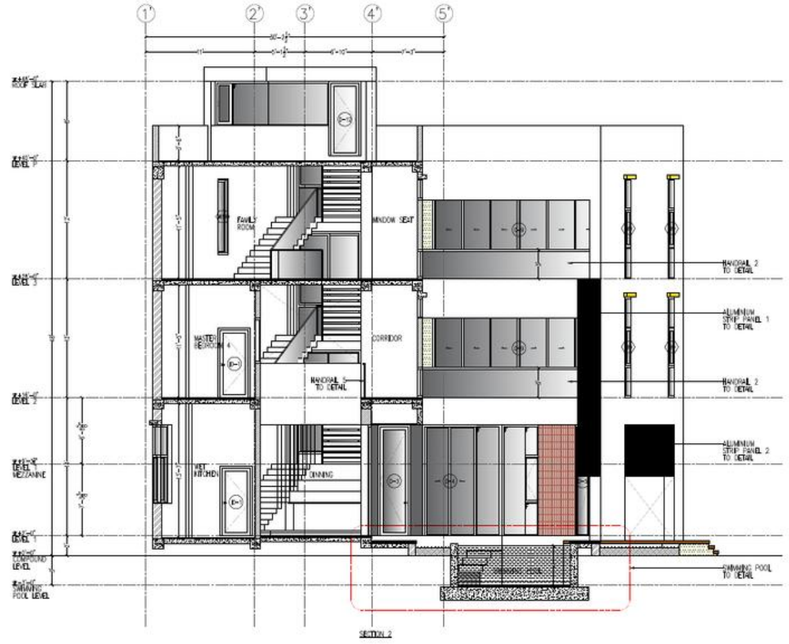
1
2
3
4
5
FAMILY ROOM
WINDOW SEAT
MASTER BEDROOM
CORRIDOR
WET KITCHEN
RAILING 2 TO DETAIL
ALUMINUM STRIP PANEL 1 TO DETAIL
RAILING 3 TO DETAIL
RAILING 2 TO DETAIL
ALUMINUM STRIP PANEL 2 TO DETAIL
SWIMMING POOL TO DETAIL
SECTION 2

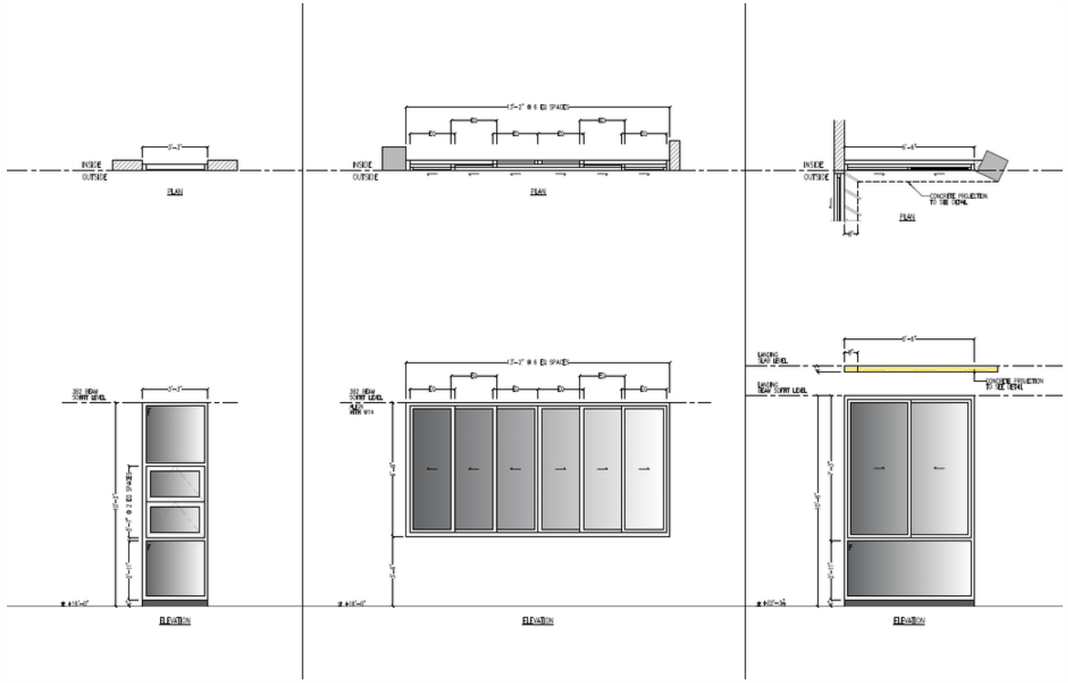
INSIDE
OUTSIDE
PLAN
PLAN
CONCRETE PROJECTION TO SEE DETAIL
PLAN
ELEVATION
ELEVATION
ELEVATION

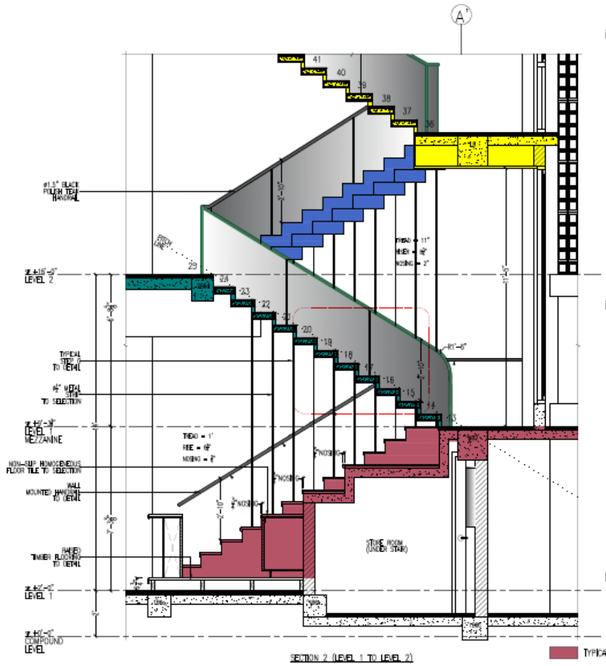
A
A'
#1.5" BLACK FULLER TEXT RAILING
TYPICAL TREAD TO DETAIL
4" RISER TYPE TO SELECTION
NON-SLIP REINFORCEMENT FLOOR TILE TO SELECTION
WALL MOUNTED HANDRAIL TO DETAIL
PAINTED TIMBER BLADDERS TO DETAIL
STONE WORK (UNDER STAIR)
TYPICAL STEP A
TYPICAL STEP B
TYPICAL STEP C
TYPICAL STEP D
SECTION 2 (LEVEL 1 TO LEVEL 2)

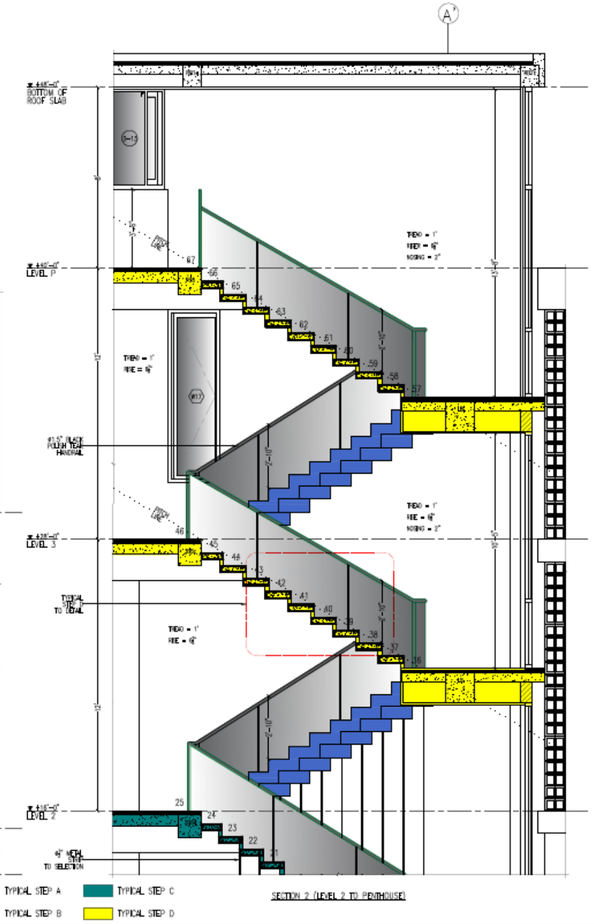
A
A'
#1.5" BLACK FULLER TEXT HANDRAIL
TYPICAL TREAD TO DETAIL
4" RISER TYPE TO SELECTION
SECTION 2 (LEVEL 2 TO PENTHOUSE)


# Project 06









- Residential Design: Three Storey  RCC Residential Building
- Location: Mandalay, Myanmar
- Software: AutoCAD 2024
- Type: Residential

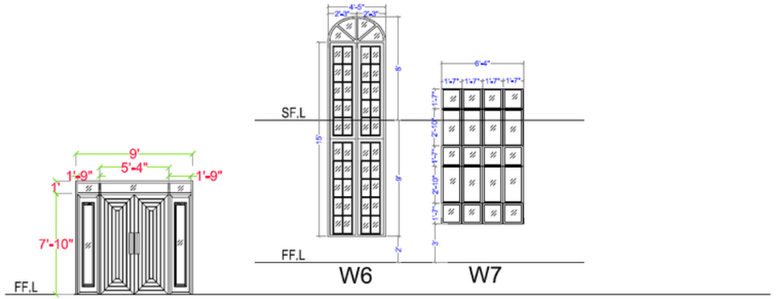


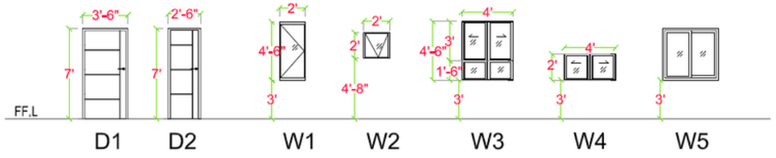


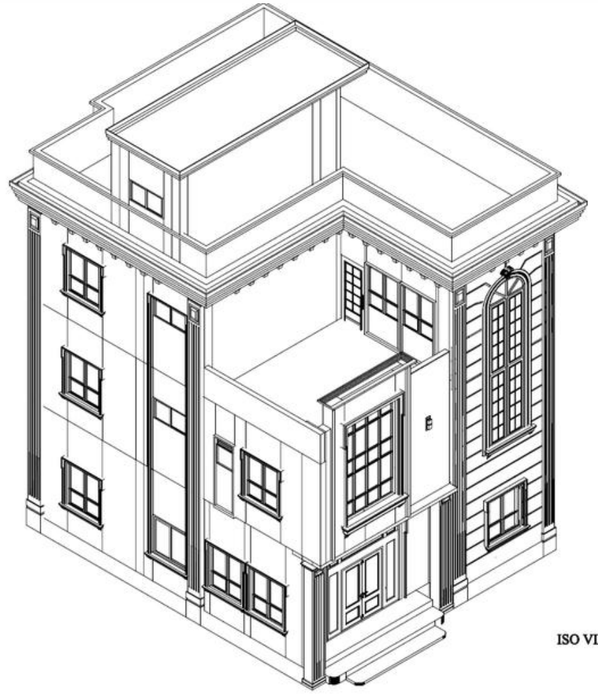

**DOOR AND WINDOW DETAILS**

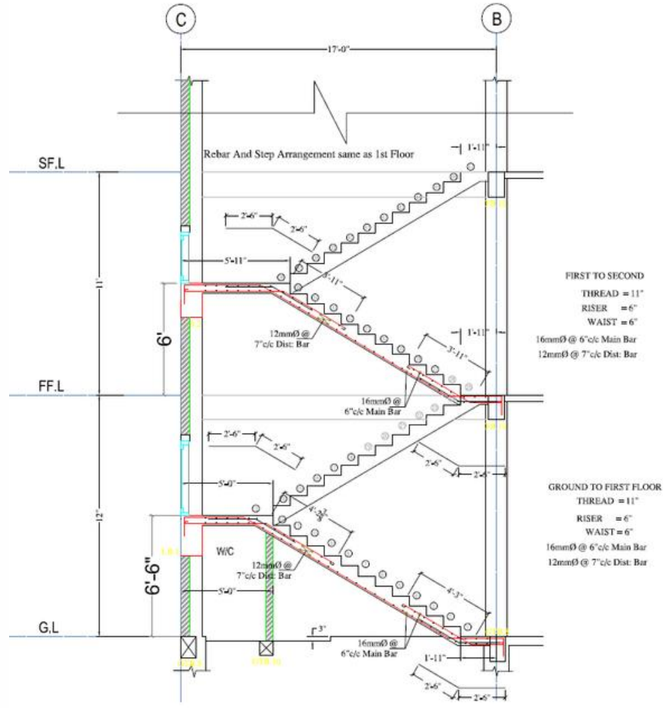


ISO VIEW

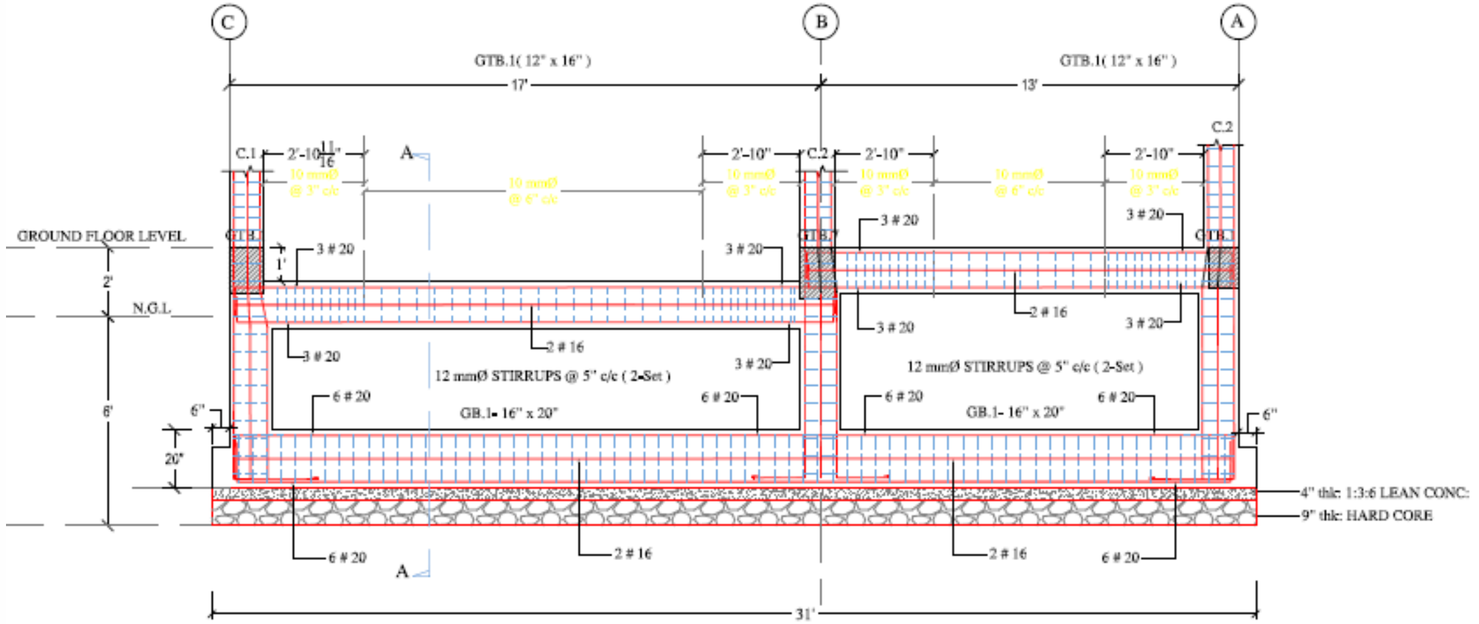


LONGITUDINAL SECTION OF GB.1 .

( SCALE ~ 1" = 4'-0" )

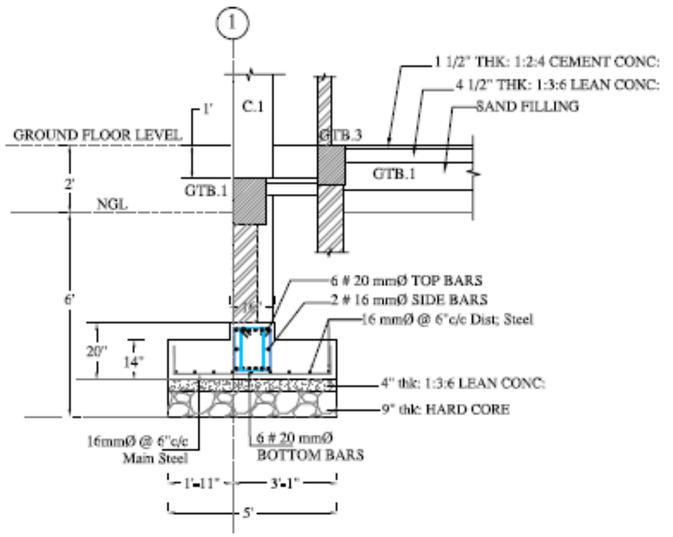




SECTION: A-A


( SCALE ~ 1" = 4'-0" )

# Project 07

- Residential Design:  Five Storey Hotel Project
- Project Type: Personal Project
- Location: Myanmar
- Software: AutoCAD 2024
- Type: Residential

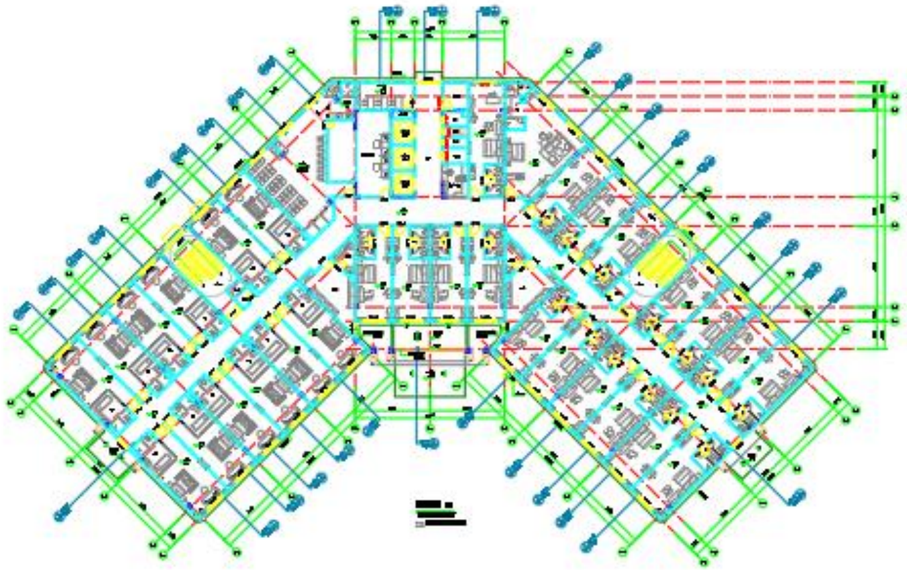


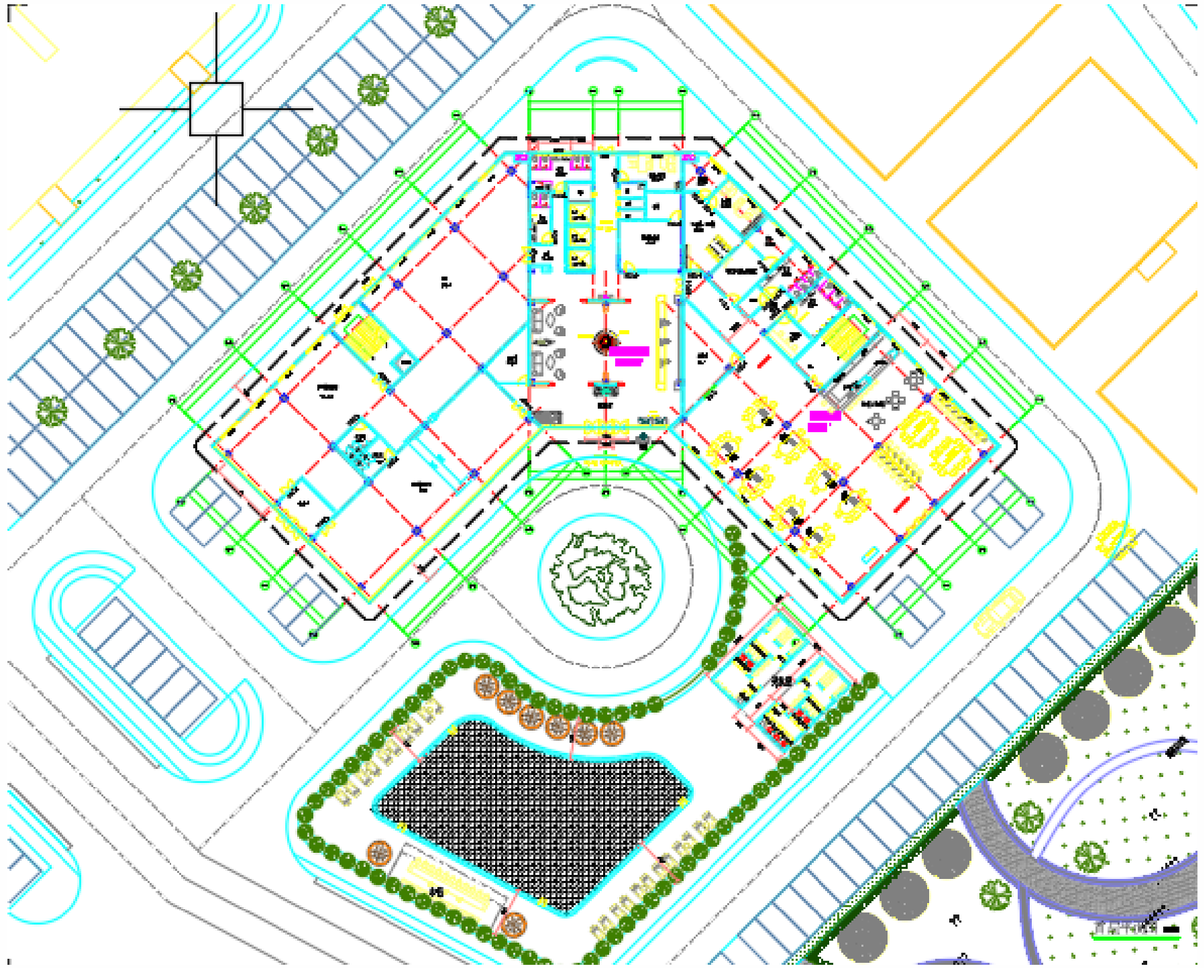


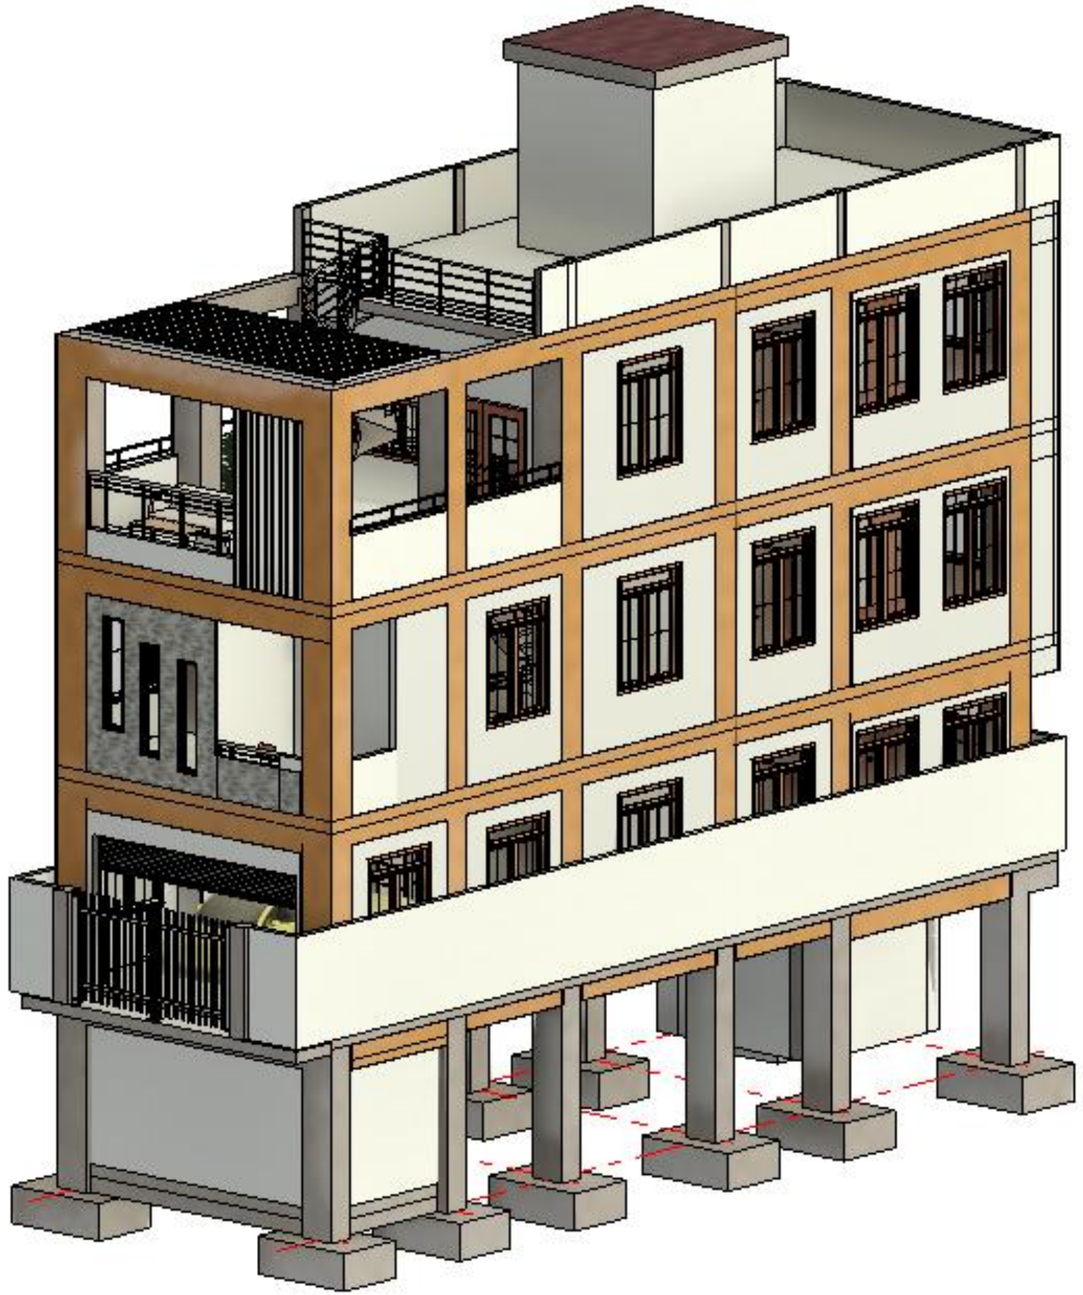



# Project 08

- Residential Design: Three and Half Stories Residential Building
- Project Type: Personal Project
- Location: Myanmar
- Software: Autodesk Revit 2024
- Type: Residential

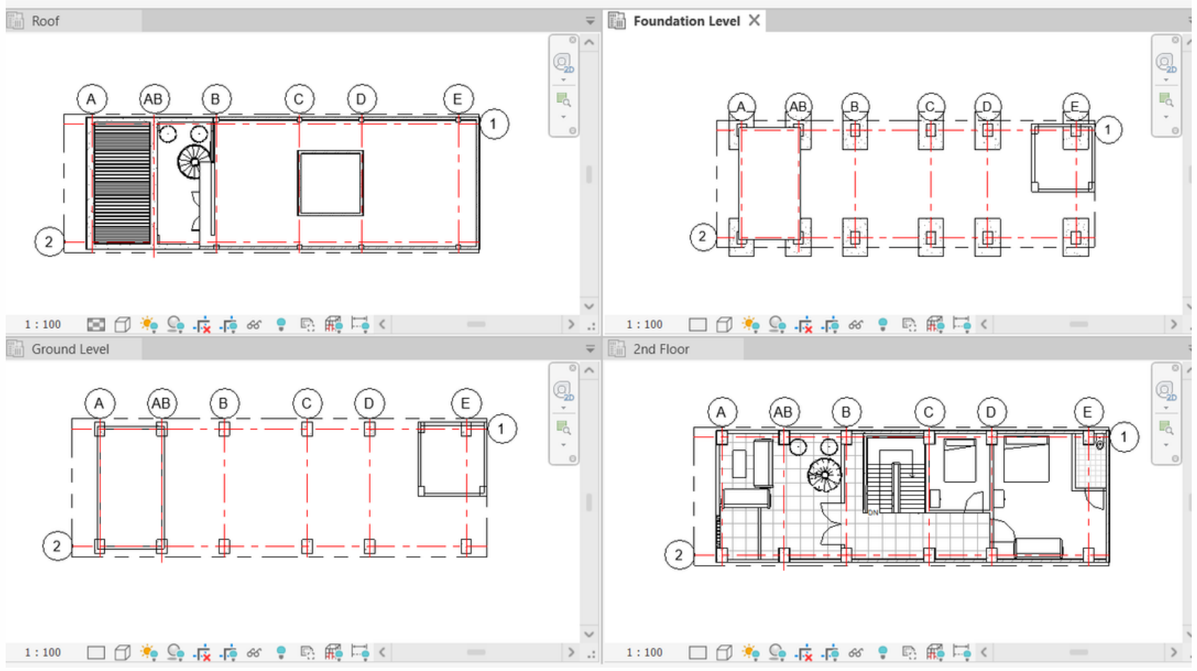
Roof
Foundation Level
Ground Level
2nd Floor
A
AB
B
C
D
E
1
2
1 : 100

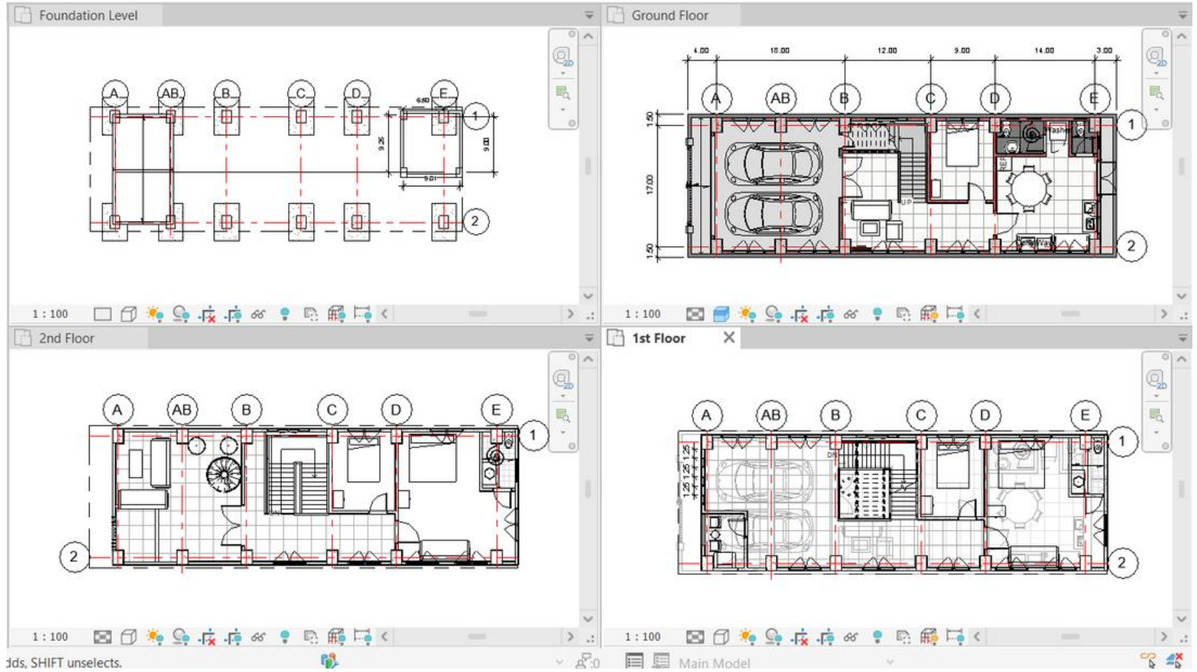
Foundation Level
Ground Floor
2nd Floor
1st Floor
A
AB
B
C
D
E
1
2
1 : 100
Main Model

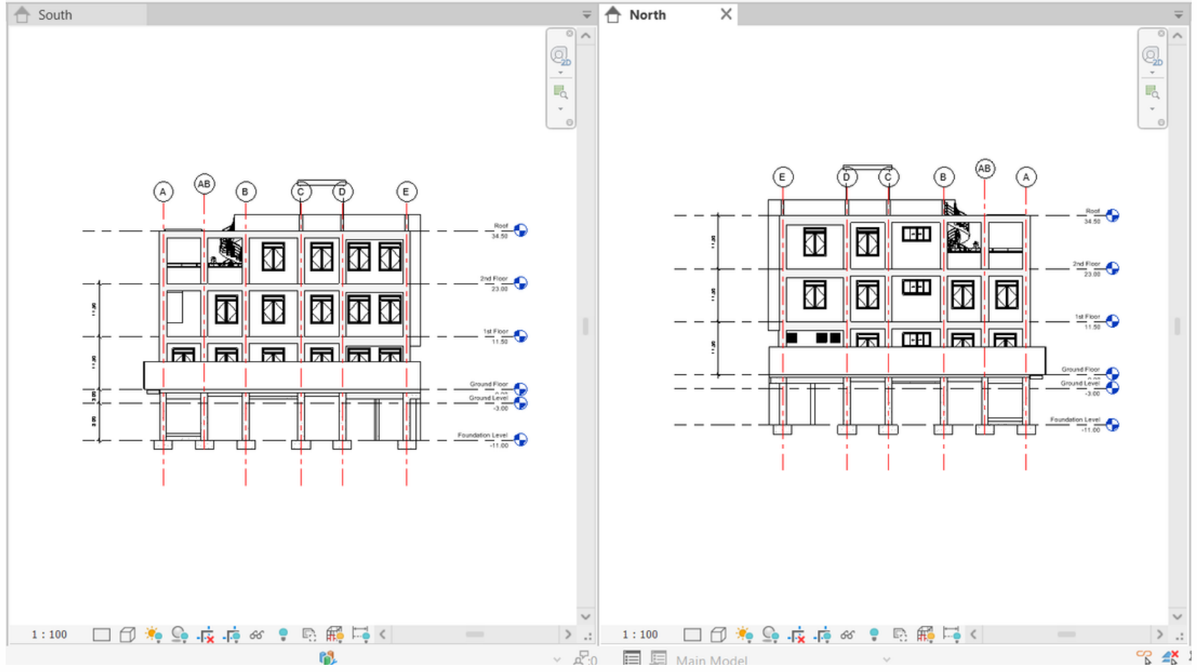
South
North
A
AB
B
C
D
E
Roof
34.50
2nd Floor
23.00
1st Floor
11.50
Ground Floor
0.00
Ground Level
-3.00
Foundation Level
-11.00
1 : 100
Main Model

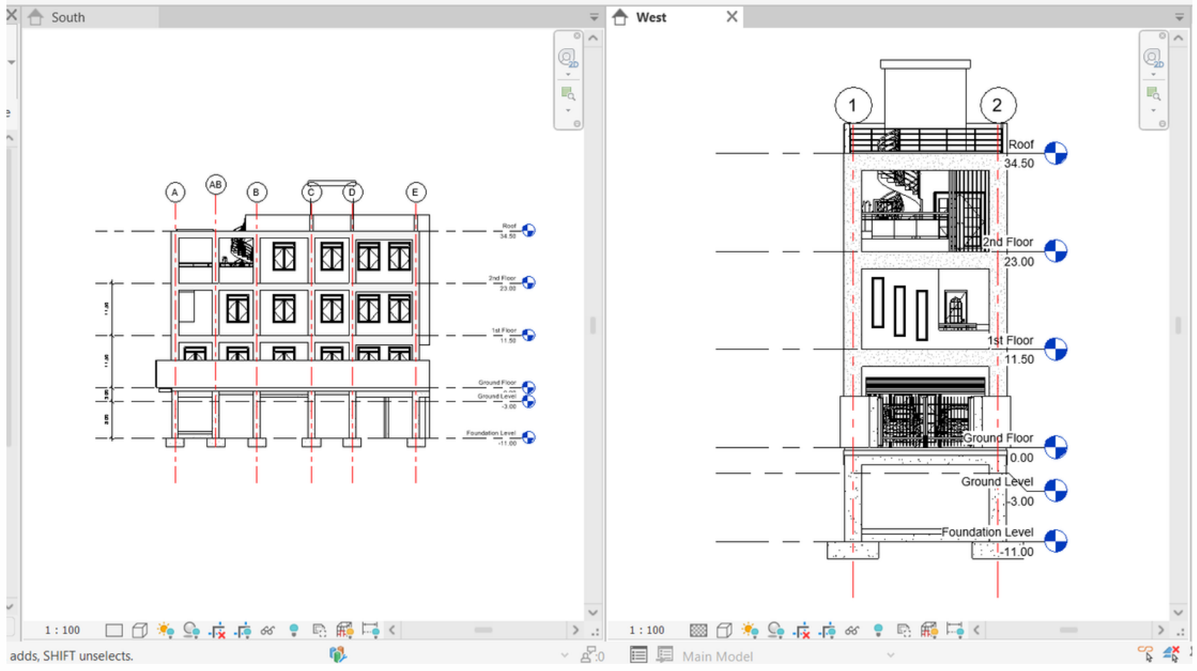
South
West
A
AB
B
C
D
E
1
2
Roof
34.50
2nd Floor
23.00
1st Floor
11.50
Ground Floor
0.00
Ground Level
-3.00
Foundation Level
-11.00
1 : 100
Main Model

# Project 09

- Project : Mix Used Building Project
- Location: Myanmar
- Software: Autodesk Revit 2024
- Type: Residential





Garden



Swimming Pool




Entrance




Entrance




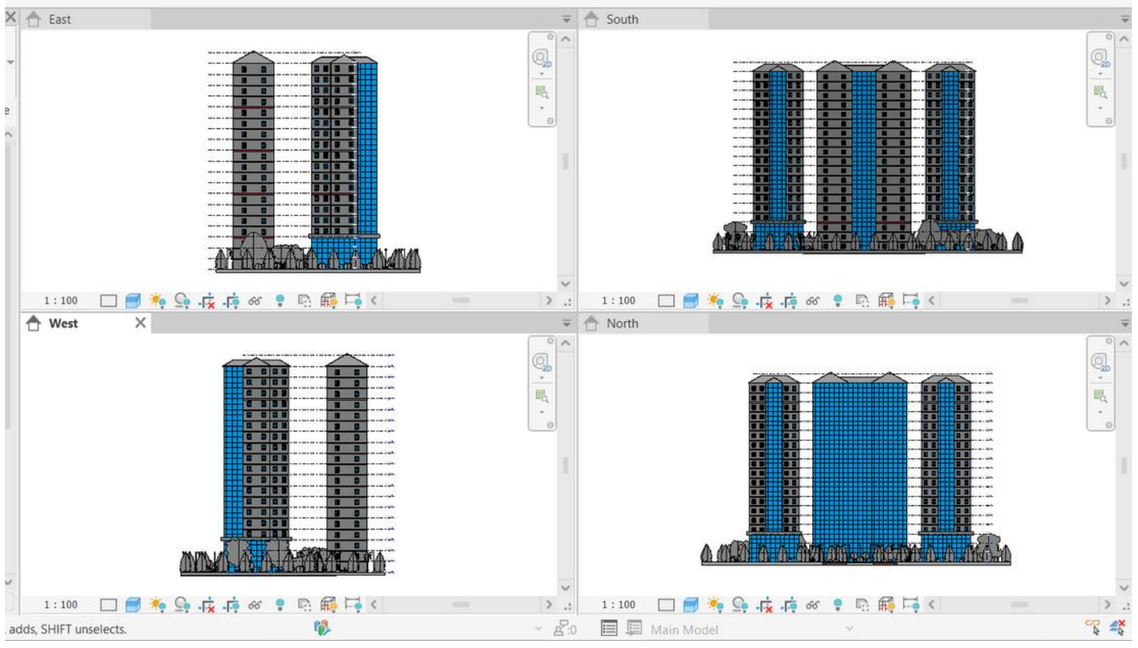



East
South
West
North
1 : 100
adds, SHIFT unselects.
Main Model

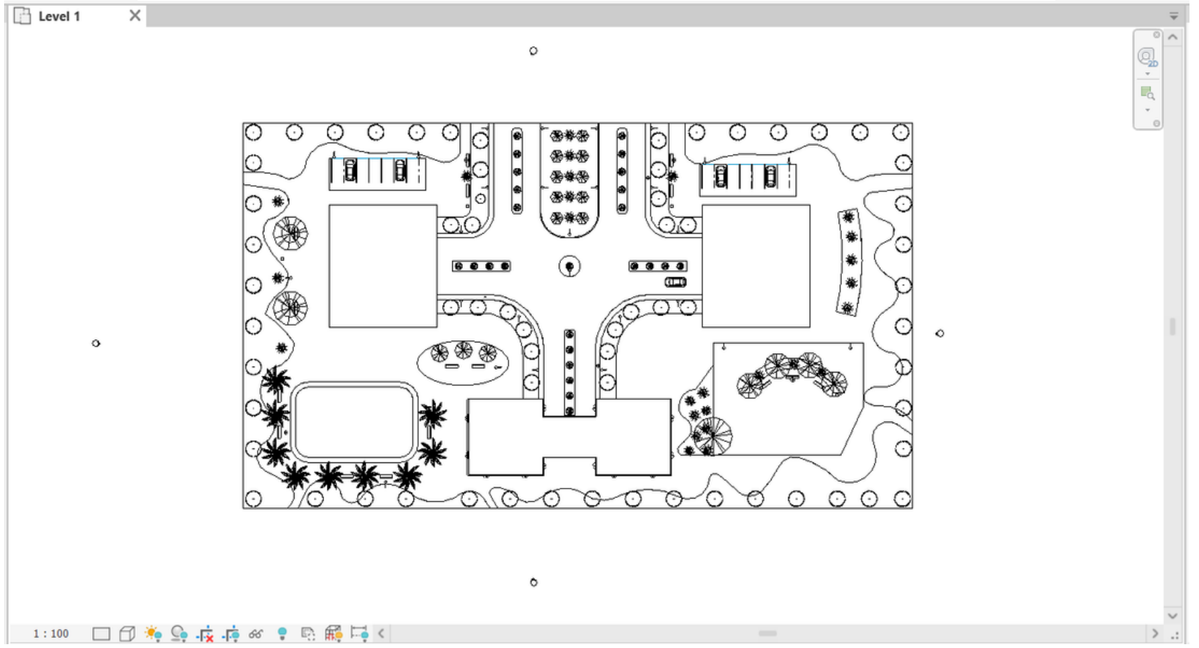
Level 1
1 : 100

# Project 10

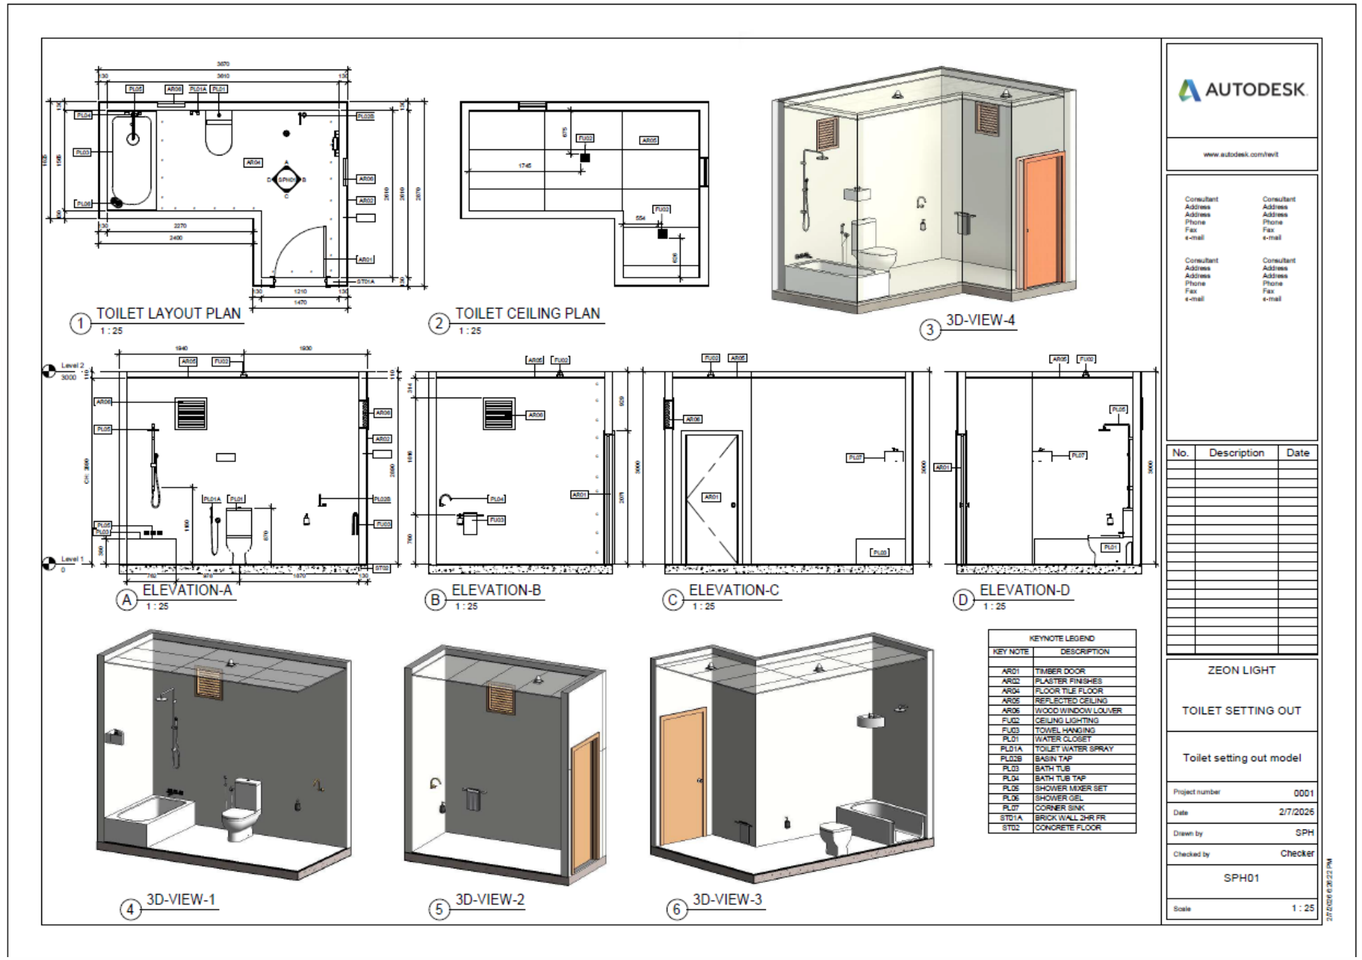



- Project : Toilet Setting Out
- Software: Autodesk Revit 2024

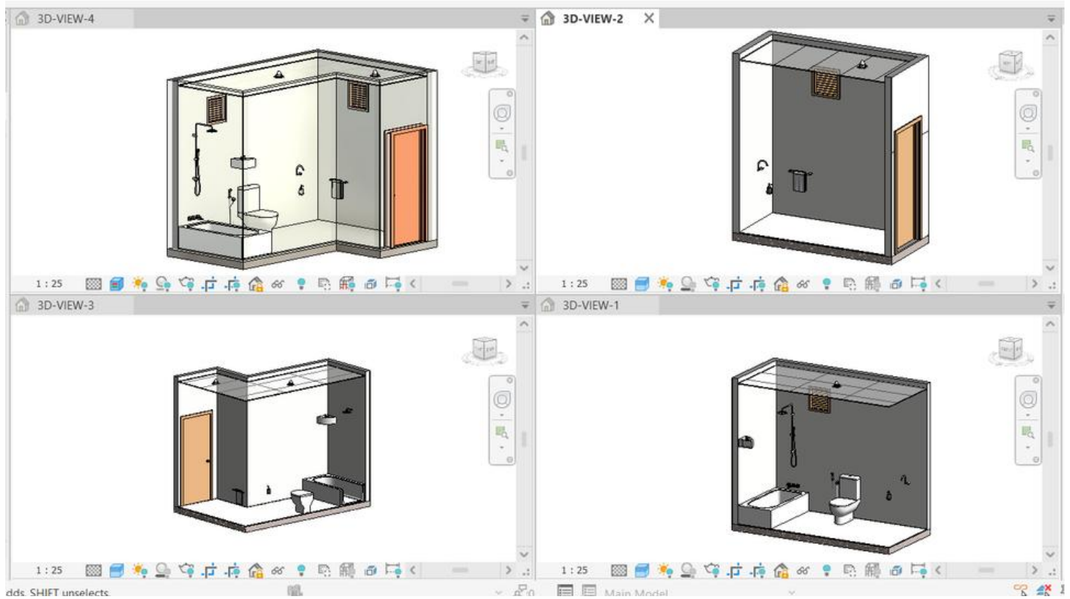






# Project 11

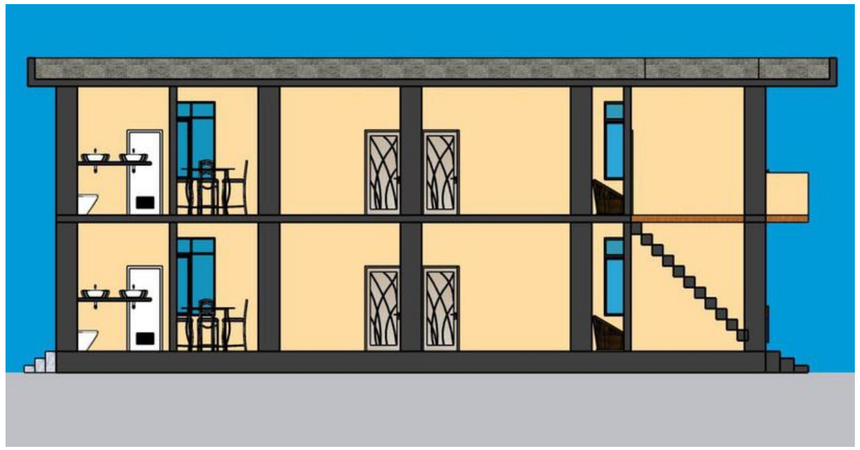

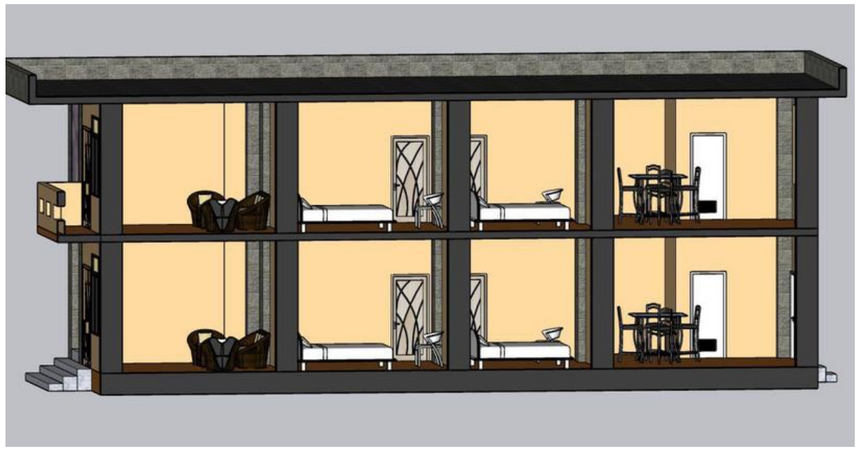


- Residential Design: Two Storey Building Project
- Project Type: Personal Project
- Location: Myanmar
- Software: Sketchup 2024
- Type: Residential








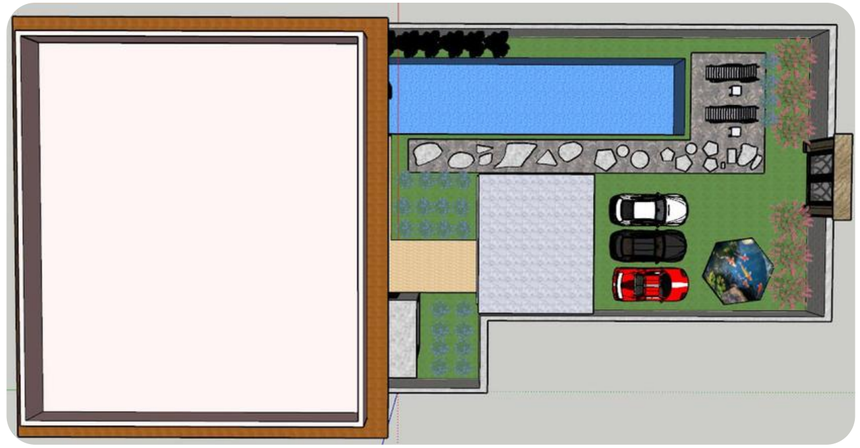

# Project 12

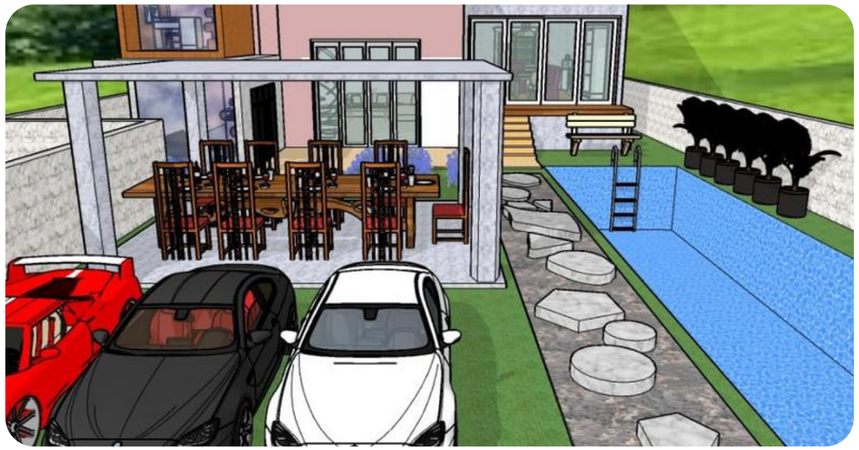



- Design: Guest House – Exterior 3D Modelling
- Project Type: Academic Project
- Location: Myanmar
- Software: Sketchup 2024
- Type: Residential






welcome to
GUEST
HOUSE
perfect for your trip



# Project 13

- Project name - Monastery
- Location: Myanmar
- Software: Sketchup 2024





# 14. Other Projects

- Software: SketchUp 2024
- Project: Interior Design Animation Video










# 14. Other Projects

- Software: Tekla Structural Designer 2025
- Project Type: Training Project
- Scope: 3D Structural Modeling & Basic Structural Analysis

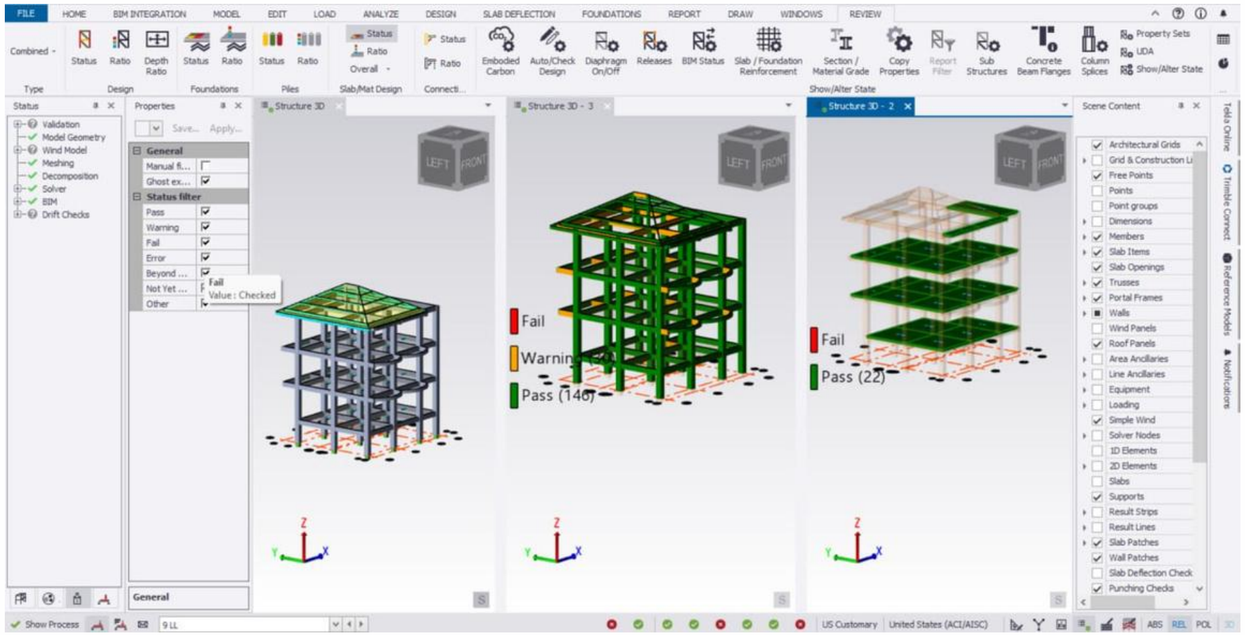

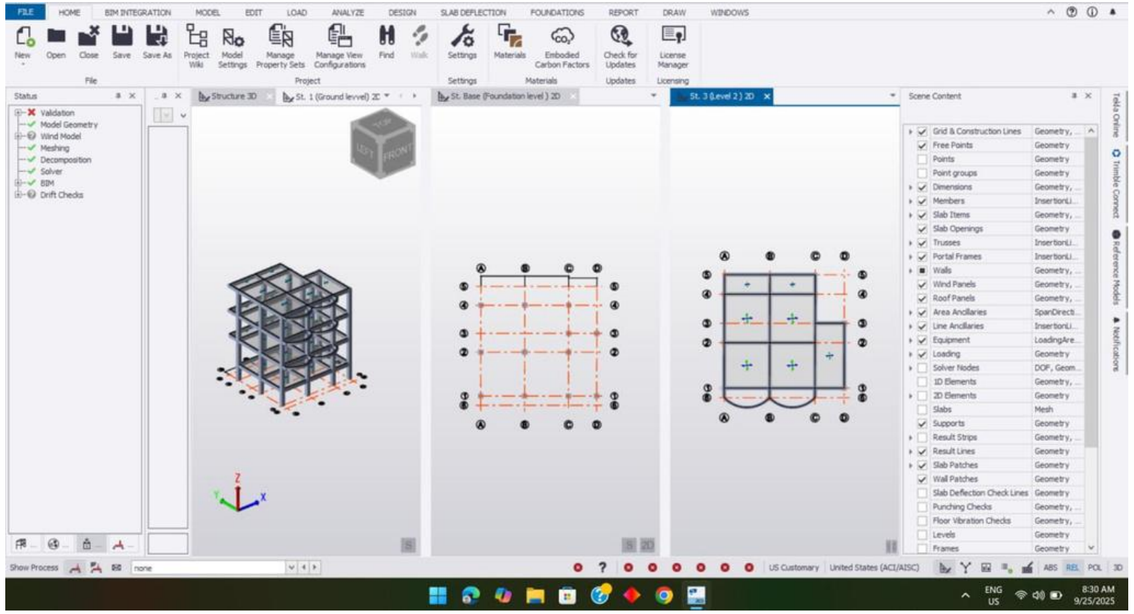
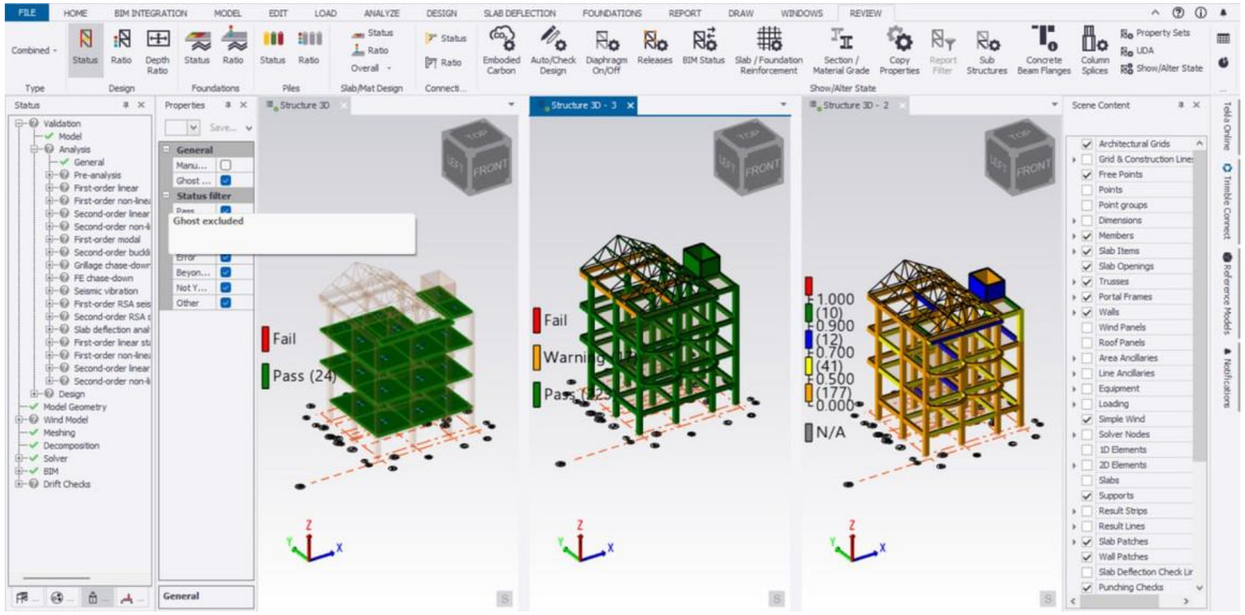
# PROFESSIONAL DEVELOPMENT

CONTINUOUS LEARNING & SKILL DEVELOPMENT

## 01 / PROFESSIONAL TRAINING

1.BIM Level 01 – Architecture & Structure

- BIM Modeling (Architecture & Structure)
- Revit Family & Component Library Creation
- BIM Documentation & Data Extraction
- Collaboration Tools & Worksharing

1.BIM Level 02 – Advanced Architectural BIM

- Advanced Architectural BIM Modeling
- Conceptual & Parametric Modeling
- Dynamo Visual Programming
- Interior, Exterior & Landscape Modeling
- Visualization, Rendering & Documentation

1.Chinese (Mandarin)

- Speaking
- Listening

## 02 / CURRENTLY DEVELOPING SKILLS (SOFTWARE & TECHNICAL SKILLS)

AUTODESK Revit

AUTODESK Navisworks Manage

Dynamo

# THANK YOU

FOR REVIEWING MY PORTFOLIO

Drafter | BIM Modeler

Architectural Drafting • BIM Modeling • 3D Visualization

**BETTER DESIGNS FOR A BRIGHTER TOMORROW**

SEIN PYAE HTAY

pyaepyae205200@gmail.com | +959 400523608 (Whatsapp) | https://www.linkedin.com/in/sein-pyae-htay